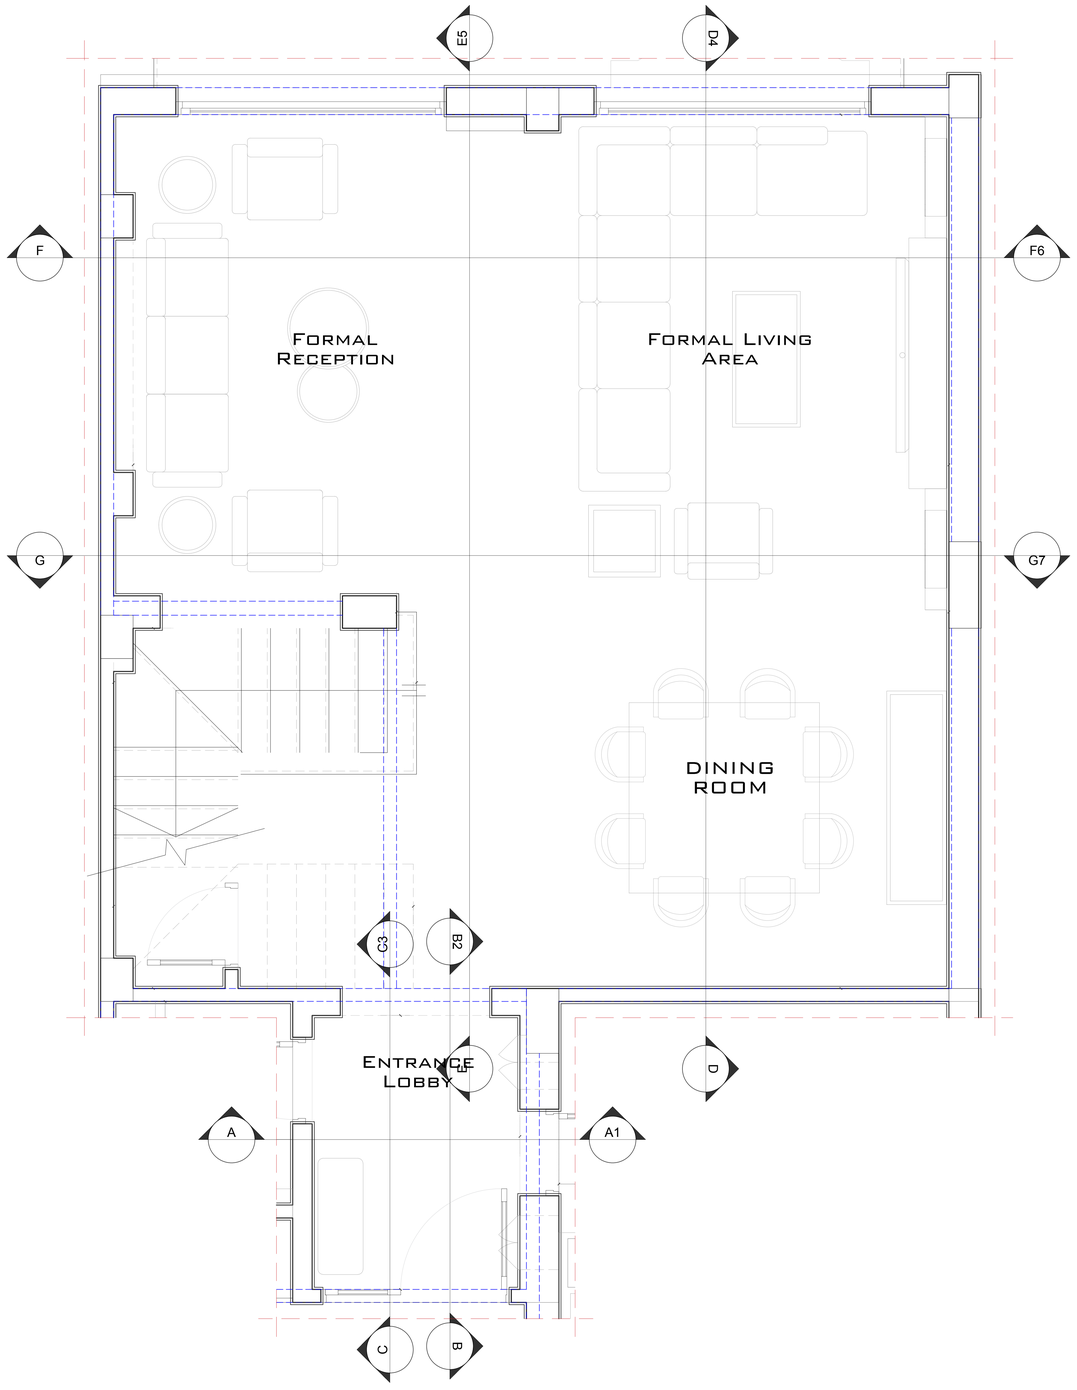

15 RECEPTION PLAN

مسقط افقى للريسيبشن

THD STUDIO
www.THDstudio.net

CLIENT:
ا / ايناس البيلى
MRS. Inas El Beily

TITLE:
فيـــلا سكنيـــة
Residential Villa

LAVISTA DEVELOPMENTS

DRAWING :
MASTER SUITE PLAN
مسقط افقى لجناح النوم الرئيسى

DATE:	SCALE:	PAPER:
JUN, 2026	1 : 100	A0

DRAWING BY:
ENG. BAHAELDIN AHMED

REVISED BY:
ENG. ZAHRAA SALEH

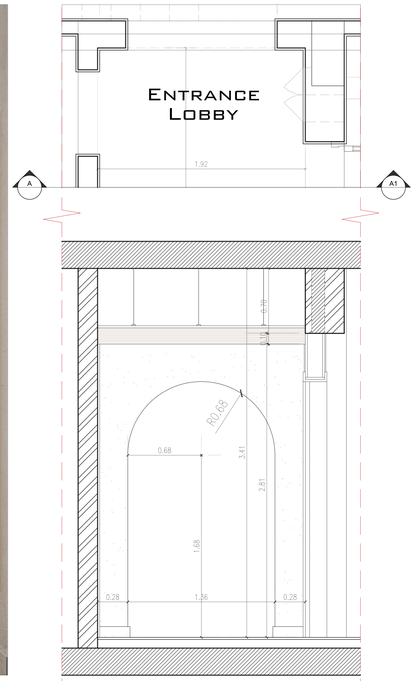

15 INTERNAL ELEVATIONS - RECEPTION

مساقط راسية - الريسيبشن

THD
STUDIO
www.THDstudio.net

CLIENT:
ا / ايناس البيلى
MRS. Inas El Beily

TITLE:
فيـــلا سكنيـــة
Residential Villa

LAVISTA DEVELOPMENTS

DRAWING :
INTERNAL ELEVATIONS
مساقط راسية

DATE:	SCALE:	PAPER:
JUN, 2026	1 : 100	A0

DRAWING BY:
ENG. BAHAELDIN AHMED

REVISED BY:
ENG. ZAHRAA SALEH

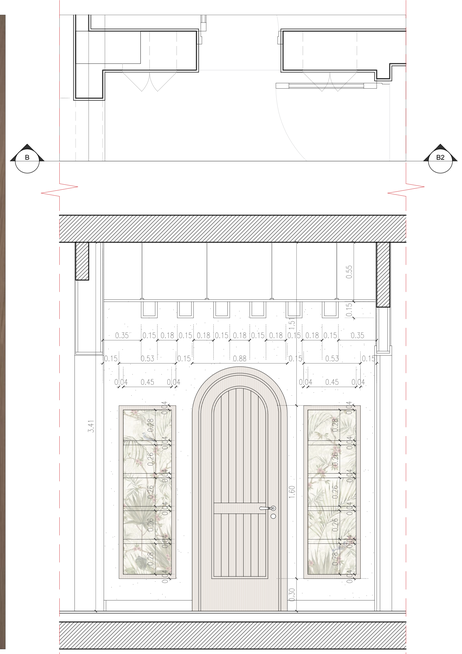

15 INTERNAL ELEVATIONS - RECEPTION

مساقط راسية - الريسيبشن

THD
STUDIO
www.THDstudio.net

CLIENT:
ا / ايناس البيلى
MRS. Inas El Beily

TITLE:
فيـــلا سكنيـــة
Residential Villa

LAVISTA DEVELOPMENTS

DRAWING :
INTERNAL ELEVATIONS
مساقط راسية

DATE:	SCALE:	PAPER:
JUN, 2026	1 : 100	A0

DRAWING BY:
ENG. BAHAELDIN AHMED

REVISED BY:
ENG. ZAHRAA SALEH

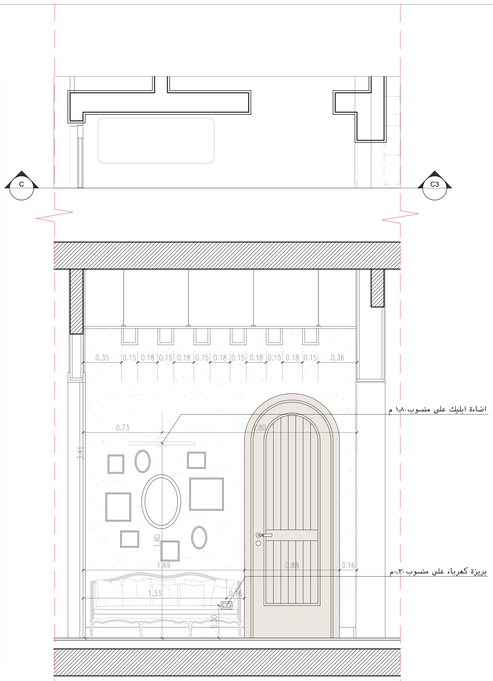

15 INTERNAL ELEVATIONS - RECEPTION

مساقط راسية - الريسيبشن

THD
STUDIO
www.THDstudio.net

CLIENT:
ا / ايناس البيلى
MRS. Inas El Beily

TITLE:
فيـــلا سكنيـــة
Residential Villa

LAVISTA DEVELOPMENTS

DRAWING :
INTERNAL ELEVATIONS
مساقط راسية

DATE:	SCALE:	PAPER:
JUN, 2026	1 : 100	A0

DRAWING BY:
ENG. BAHAELDIN AHMED

REVISED BY:
ENG. ZAHRAA SALEH

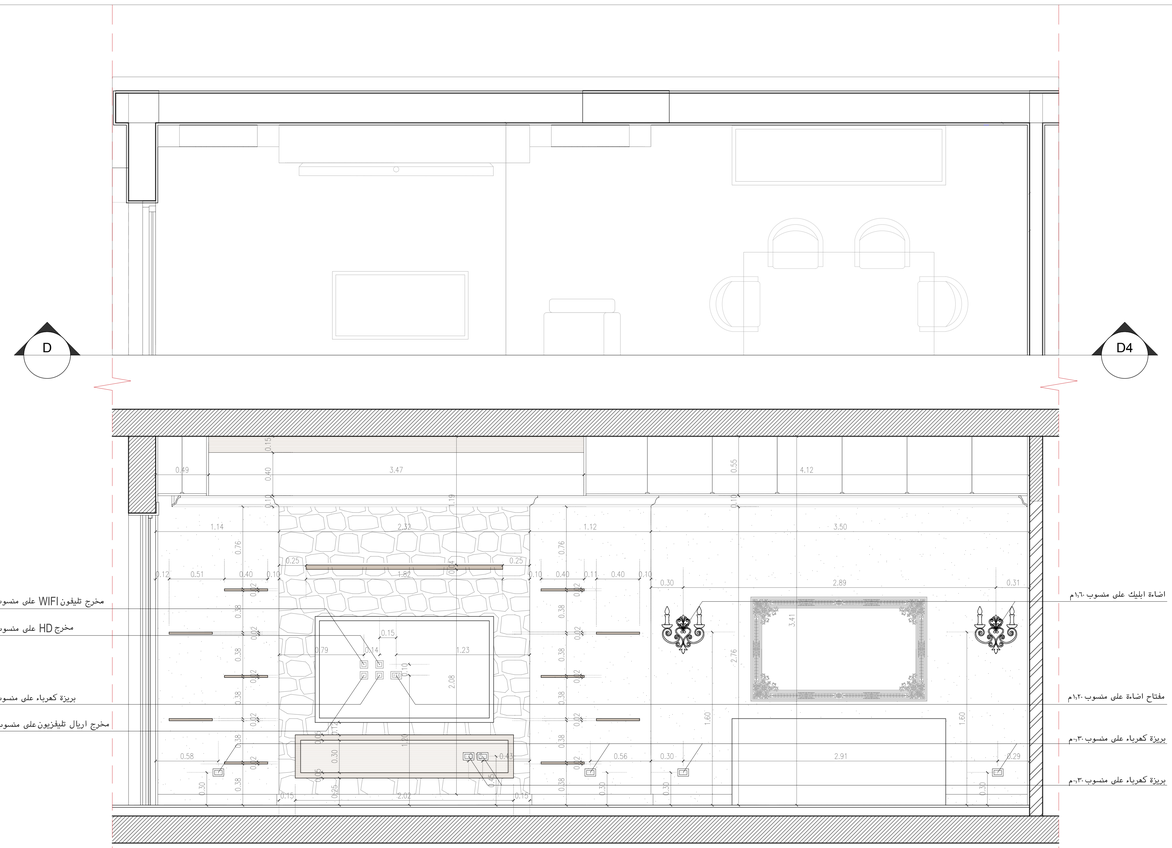

INTERNAL ELEVATIONS - RECEPTION

مساقط راسية - الريسيبشن

THD
STUDIO
www.THDstudio.net

CLIENT:
ا / ايناس البيلى
MRS. Inas El Beily

TITLE:
فيـــلا سكنيـــة
Residential Villa

LAVISTA DEVELOPMENTS

DRAWING :
INTERNAL ELEVATIONS
مساقط راسية

DATE:	SCALE:	PAPER:
JUN, 2026	1 : 100	A0

DRAWING BY:
ENG. BAHAELDIN AHMED

REVISED BY:
ENG. ZAHRAA SALEH

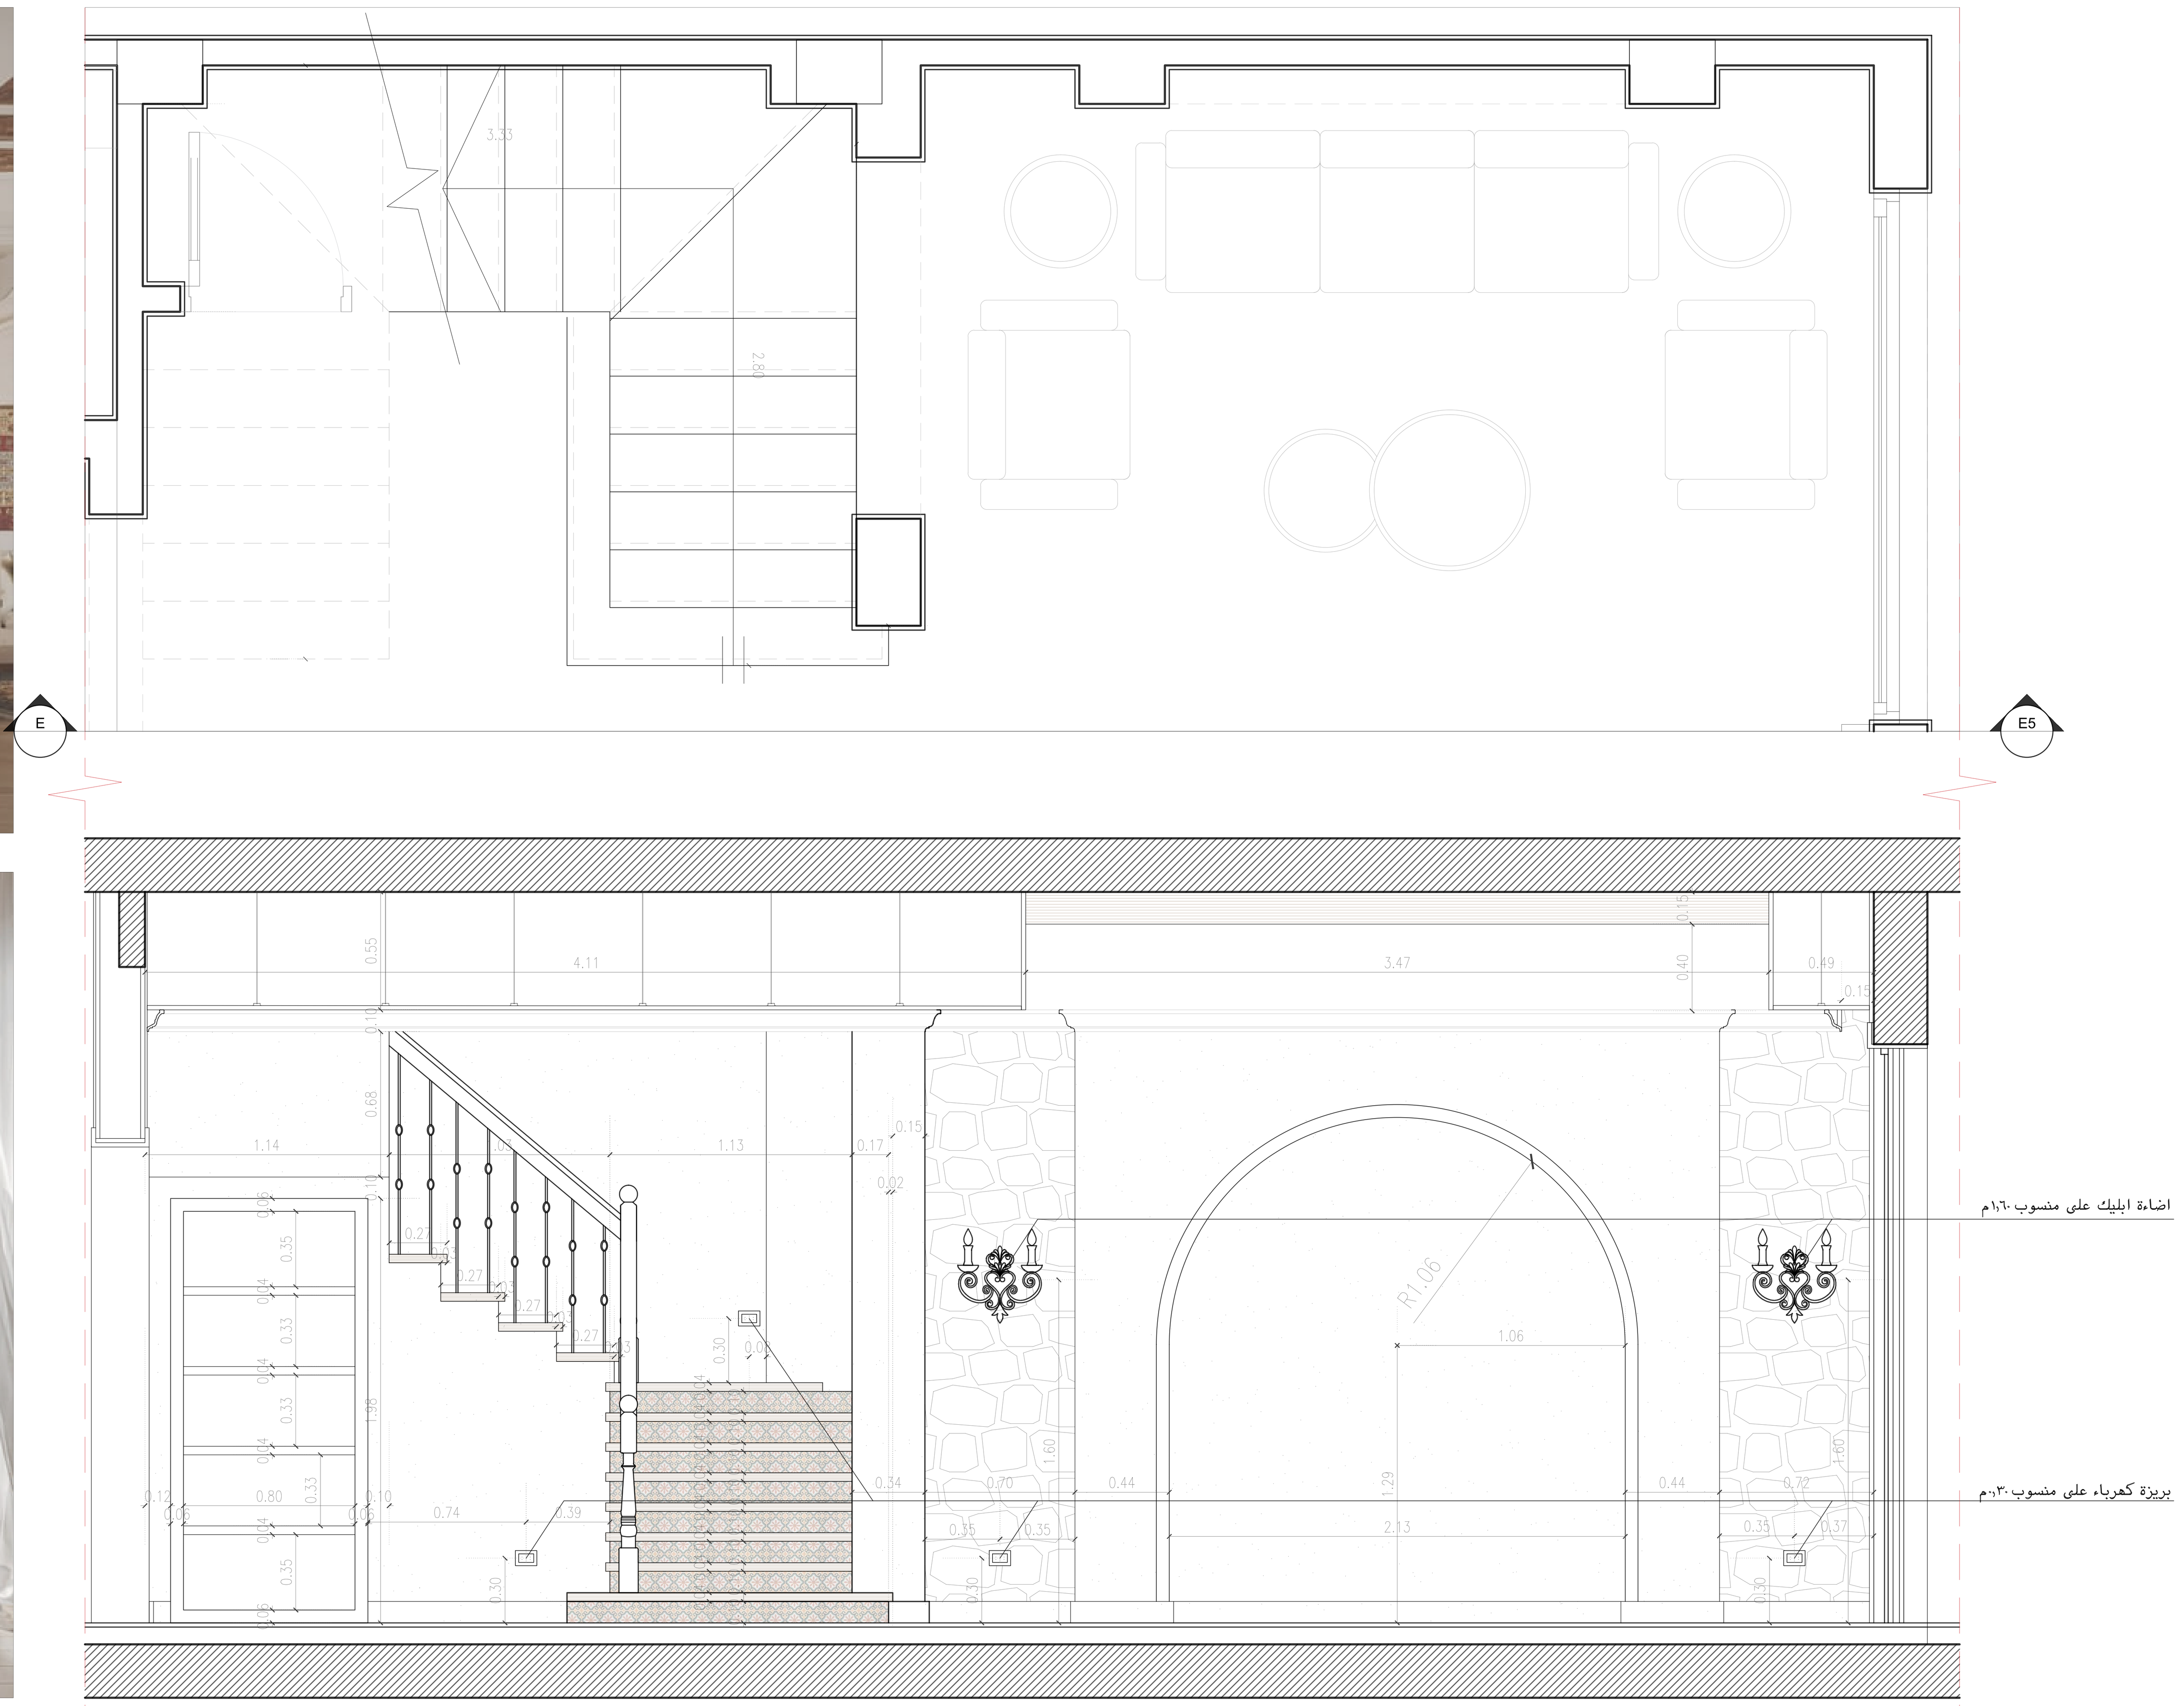

15 INTERNAL ELEVATIONS - RECEPTION

مساقط راسية - الريسيبشن

THD STUDIO
www.THDstudio.net

CLIENT:
ا / ايناس البيلى
MRS. Inas El Beily

TITLE:
فيــــلا سكنيــــة
Residential Villa

LAVISTA DEVELOPMENTS

DRAWING :
INTERNAL ELEVATIONS
مساقط راسية

DATE:	SCALE:	PAPER:
JUN, 2026	1 : 100	A0

DRAWING BY:
ENG. BAHAELDIN AHMED

REVISED BY:
ENG. ZAHRAA SALEH

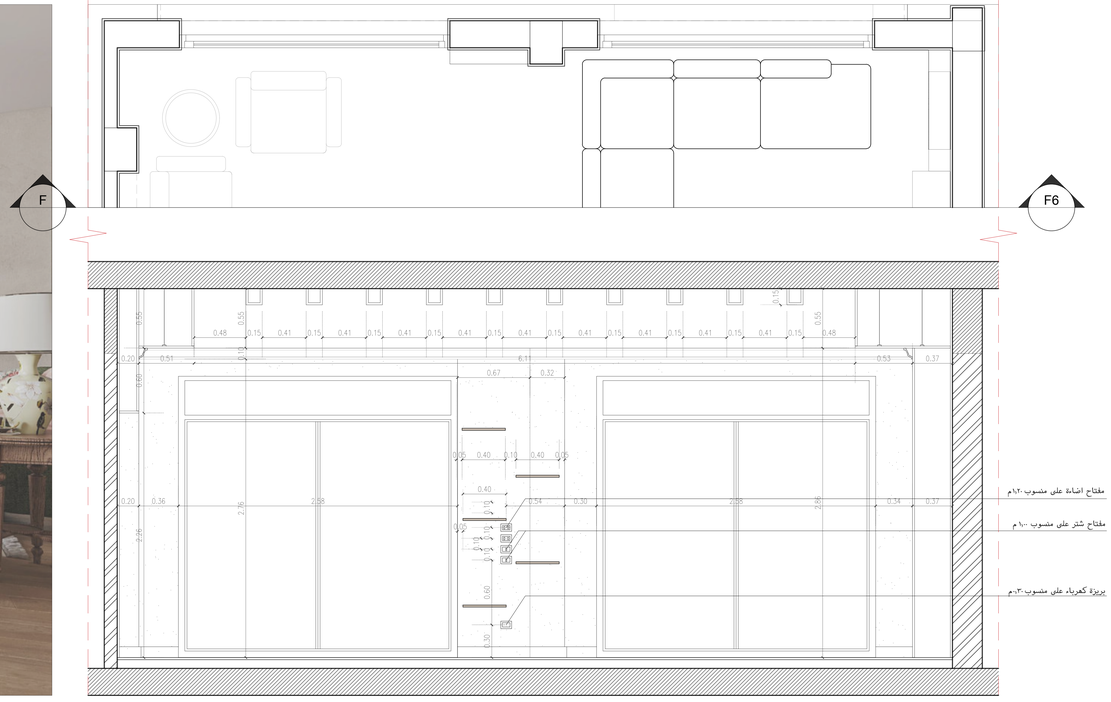

15 INTERNAL ELEVATIONS - RECEPTION

مساقط راسية - الريسيبشن

THD STUDIO
www.THDstudio.net

CLIENT:
ا / ايناس البيلى
MRS. Inas El Beily

TITLE:
فيـــلا سكنيـــة
Residential Villa

LAVISTA DEVELOPMENTS

DRAWING :
INTERNAL ELEVATIONS
مساقط راسية

DATE:	SCALE:	PAPER:
JUN, 2026	1 : 100	A0

DRAWING BY:
ENG. BAHAELDIN AHMED

REVISED BY:
ENG. ZAHRAA SALEH

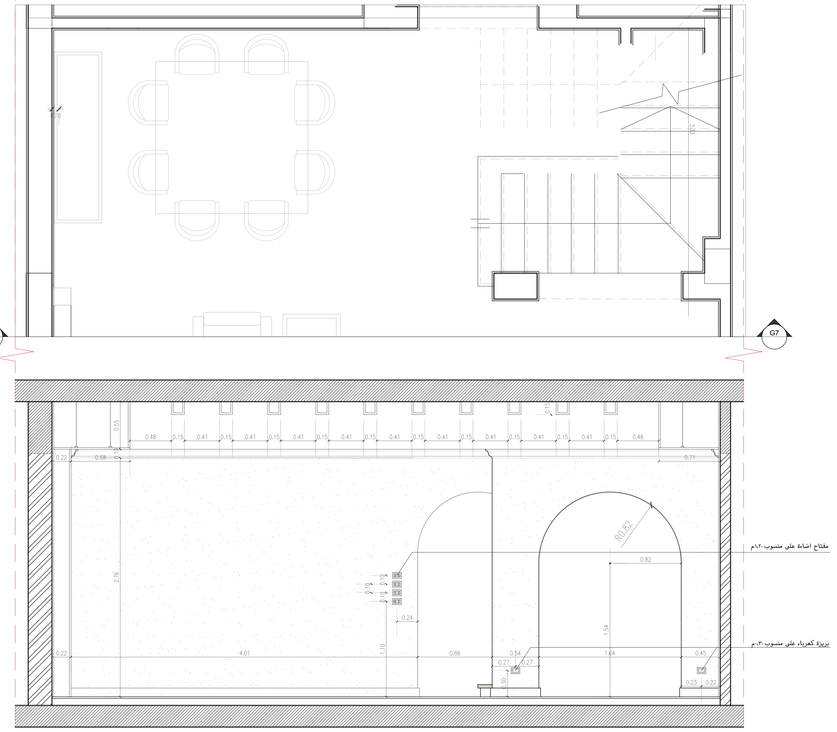

15 INTERNAL ELEVATIONS - RECEPTION

مساقط راسية - الريسيبشن

THD
STUDIO
www.THDstudio.net

CLIENT:
ا / ايناس البيلى
MRS. Inas El Beily

TITLE:
فيـــلا سكنيـــة
Residential Villa

LAVISTA DEVELOPMENTS

DRAWING :
INTERNAL ELEVATIONS
مساقط راسية

DATE:	SCALE:	PAPER:
JUN, 2026	1 : 100	A0

DRAWING BY:
ENG. BAHAELDIN AHMED

REVISED BY:
ENG. ZAHRAA SALEH

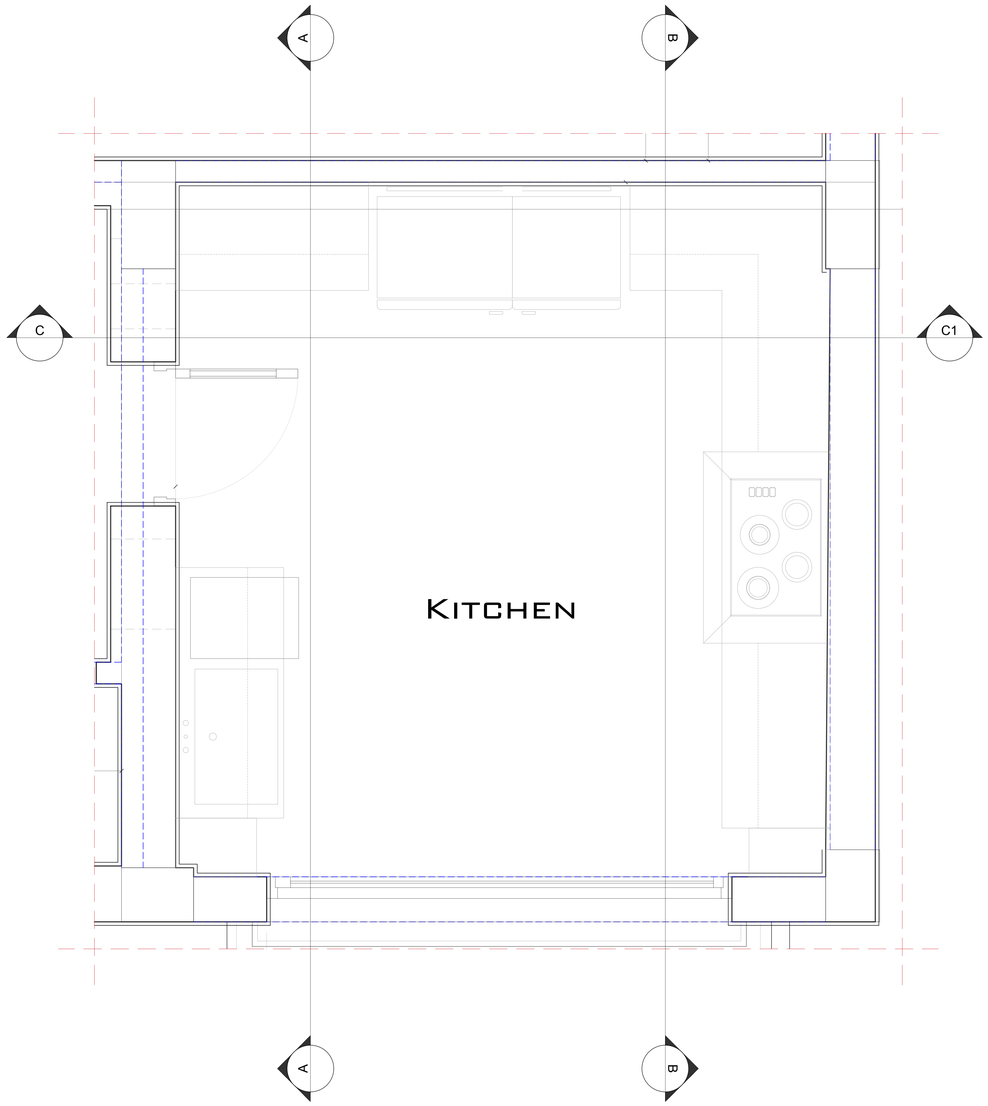

16

KITCHEN PLAN

مسقط افقى للمطبخ

THD
STUDIO
www.THDstudio.net

CLIENT:
ا/ ايناس البيلى
MRS. Inas El Beily

TITLE:
فيـــلا سكنيـــة
Residential Villa

LAVISTA DEVELOPMENTS

DRAWING :
MASTER SUITE PLAN
مسقط افقى لجناح النوم الرئيسى

DATE:	SCALE:	PAPER:
JUN, 2026	1 : 100	A0

DRAWING BY:
ENG. BAHAELDIN AHMED

REVISED BY:
ENG. ZAHRAA SALEH

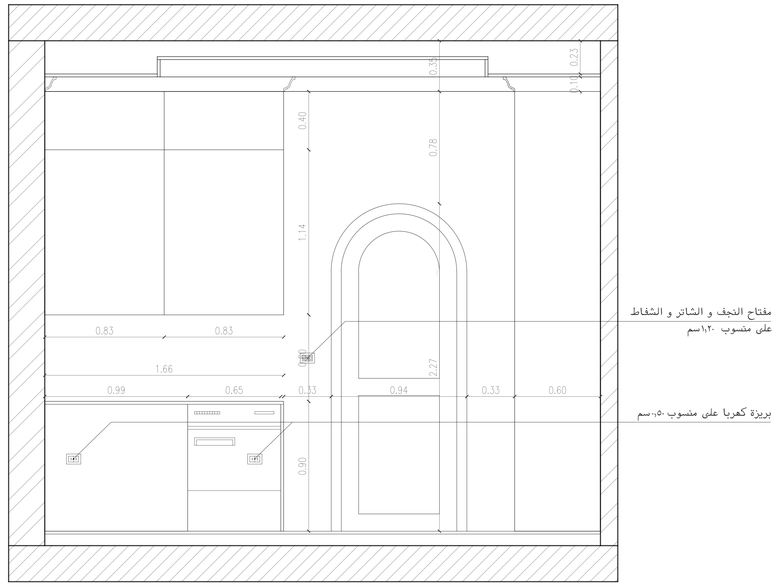

A A1

16 INTERNAL ELEVATIONS - KITCHEN

مساقط راسية - المطبخ

THD
STUDIO
www.THDstudio.net

CLIENT:
ا/ ايناس البيلى
MRS. Inas El Beily

TITLE:
فيـــلا سكنيـــة
Residential Villa

LAVISTA DEVELOPMENTS

DRAWING :
INTERNAL ELEVATIONS
مساقط راسية

DATE:	SCALE:	PAPER:
JUN, 2026	1 : 100	A0

DRAWING BY:
ENG. BAHAELDIN AHMED

REVISED BY:
ENG. ZAHRAA SALEH

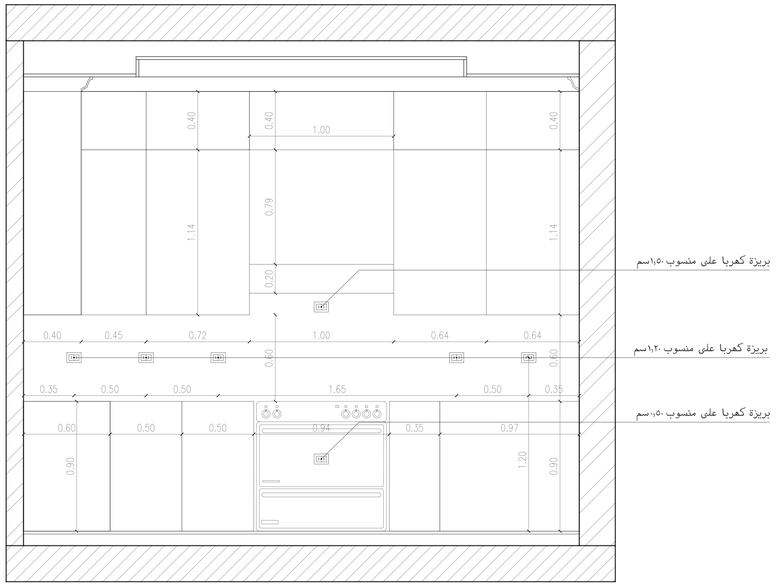

INTERNAL ELEVATIONS - KITCHEN

مساقط راسية - المطبخ

THD
STUDIO
www.THDstudio.net

CLIENT:
ا / ايناس البيلى
MRS. Inas El Beily

TITLE:
فيـــلا سكنيـــة
Residential Villa

LAVISTA DEVELOPMENTS

DRAWING :
INTERNAL ELEVATIONS
مساقط راسية

DATE:	SCALE:	PAPER:
JUN, 2026	1 : 100	A0

DRAWING BY:
ENG. BAHAELDIN AHMED

REVISED BY:
ENG. ZAHRAA SALEH

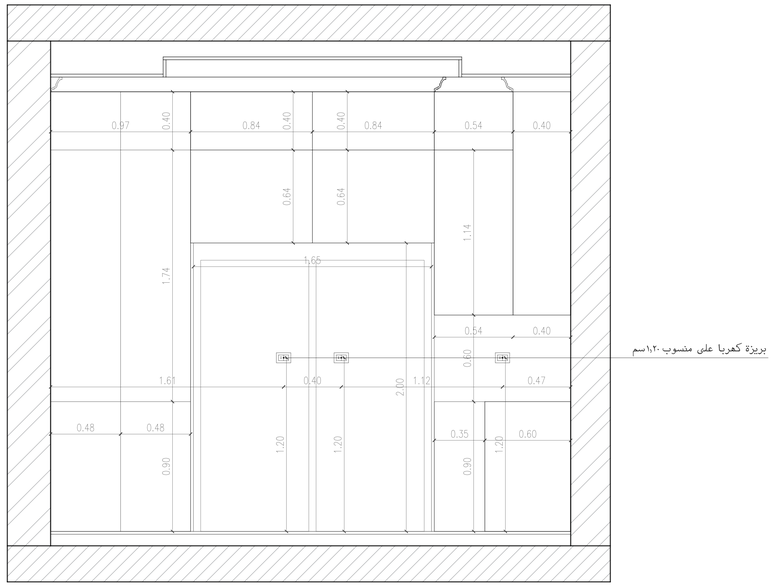

C C3

16 INTERNAL ELEVATIONS - KITCHEN

مساقط راسية - المطبخ

THD STUDIO
www.THDstudio.net

CLIENT:
ا / ايناس البيلى
MRS. Inas El Beily

TITLE:
فيـــلا سكنيـــة
Residential Villa

LAVISTA DEVELOPMENTS

DRAWING :
INTERNAL ELEVATIONS
مساقط راسية

DATE:	SCALE:	PAPER:
JUN, 2026	1 : 100	A0

DRAWING BY:
ENG. BAHAELDIN AHMED

REVISED BY:
ENG. ZAHRAA SALEH

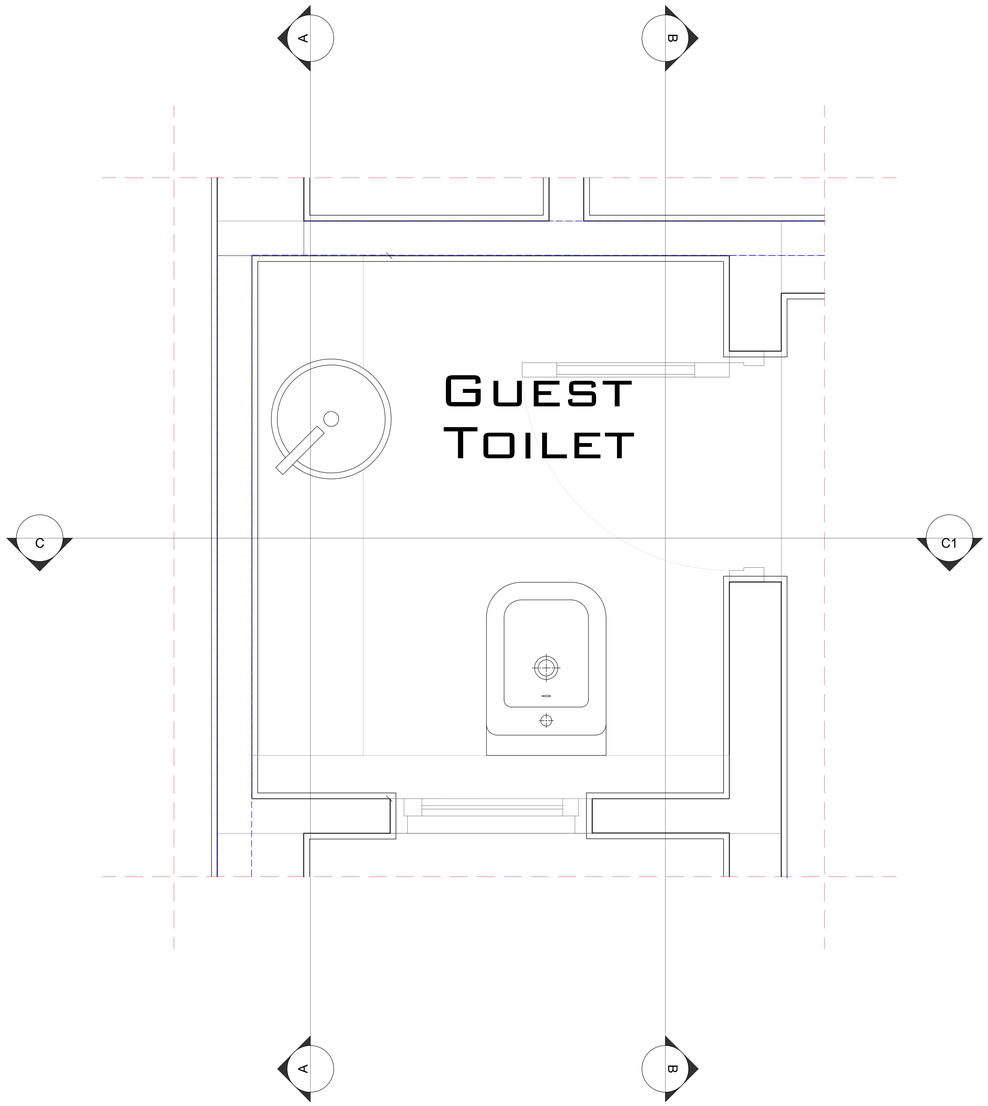

17

GUEST TOILET PLAN

مسقط افقى لحمام الضيوف

THD
STUDIO
www.THDstudio.net

CLIENT:
ا / ايناس البيلى
MRS. Inas El Beily

TITLE:
فيـــلا سكنيـــة
Residential Villa

LAVISTA DEVELOPMENTS

DRAWING :
INTERNAL ELEVATIONS
مساقط راسية

DATE:	SCALE:	PAPER:
JUN, 2026	1 : 100	A0

DRAWING BY:
ENG. BAHAELDIN AHMED

REVISED BY:
ENG. ZAHRAA SALEH

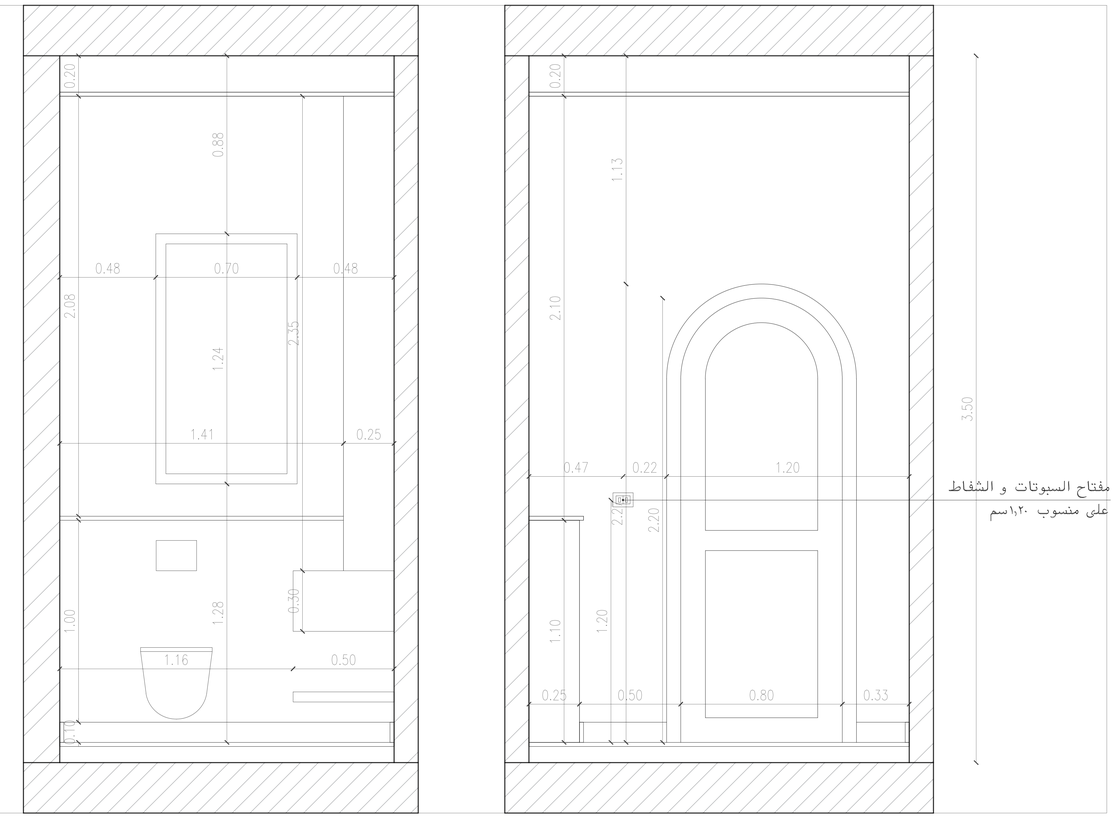

17 INTERNAL ELEVATIONS - GUEST TOILET

مساقط راسية -حمام الضيوف

THD
STUDIO
www.THDstudio.net

CLIENT:
ا / ايناس البيلى
MRS. Inas El Beily

TITLE:
فيـــلا سكنيـــة
Residential Villa

LAVISTA DEVELOPMENTS

DRAWING :
INTERNAL ELEVATIONS
مساقط راسية

DATE:	SCALE:	PAPER:
JUN, 2026	1 : 100	A0

DRAWING BY:
ENG. BAHAELDIN AHMED

REVISED BY:
ENG. ZAHRAA SALEH

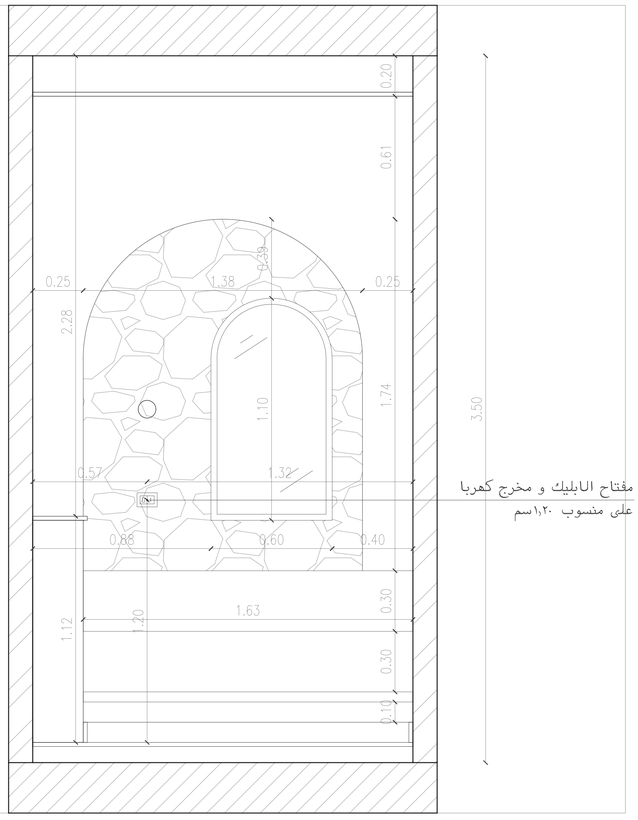

17 INTERNAL ELEVATIONS - GUEST TOILET

مساقط راسية -حمام الضيوف

THD
STUDIO
www.THDstudio.net

CLIENT:
ا/ ايناس البيلى
MRS. Inas El Beily

TITLE:
فيـــلا سكنيـة
Residential Villa

LAVISTA DEVELOPMENTS

DRAWING :
INTERNAL ELEVATIONS
مساقط راسية

DATE:	SCALE:	PAPER:
JUN, 2026	1 : 100	A0

DRAWING BY:
ENG. BAHAELDIN AHMED

REVISED BY:
ENG. ZAHRAA SALEH

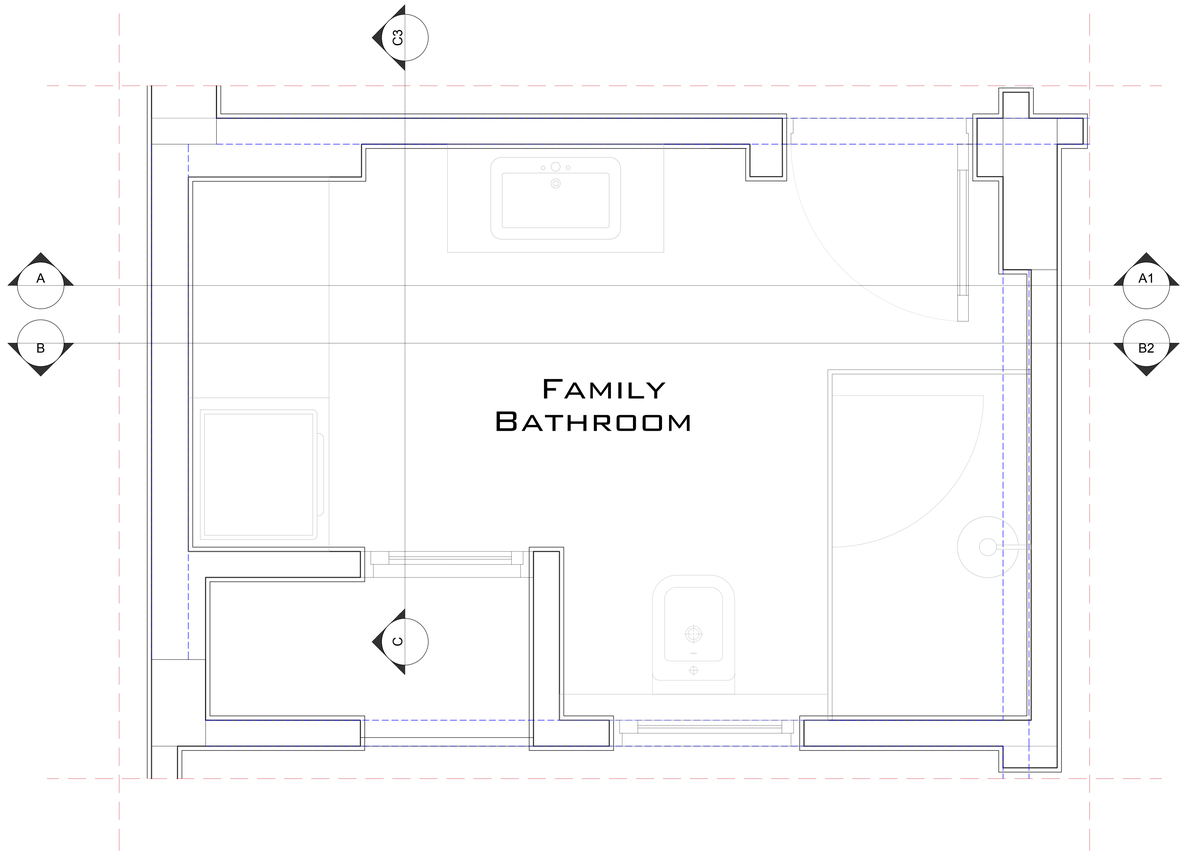

18

FAMILY BATHROOM PLAN

مسقط افقى لحمام العائلة

THD
STUDIO
www.THDstudio.net

CLIENT:
ا / ايناس البيلى
MRS. Inas El Beily

TITLE:
فيـــلا سكنيـــة
Residential Villa

LAVISTA DEVELOPMENTS

DRAWING :
MASTER SUITE PLAN
مسقط افقى لجناح النوم الرئيسى

DATE:	SCALE:	PAPER:
JUN, 2026	1 : 100	A0

DRAWING BY:
ENG. BAHAELDIN AHMED

REVISED BY:
ENG. ZAHRAA SALEH

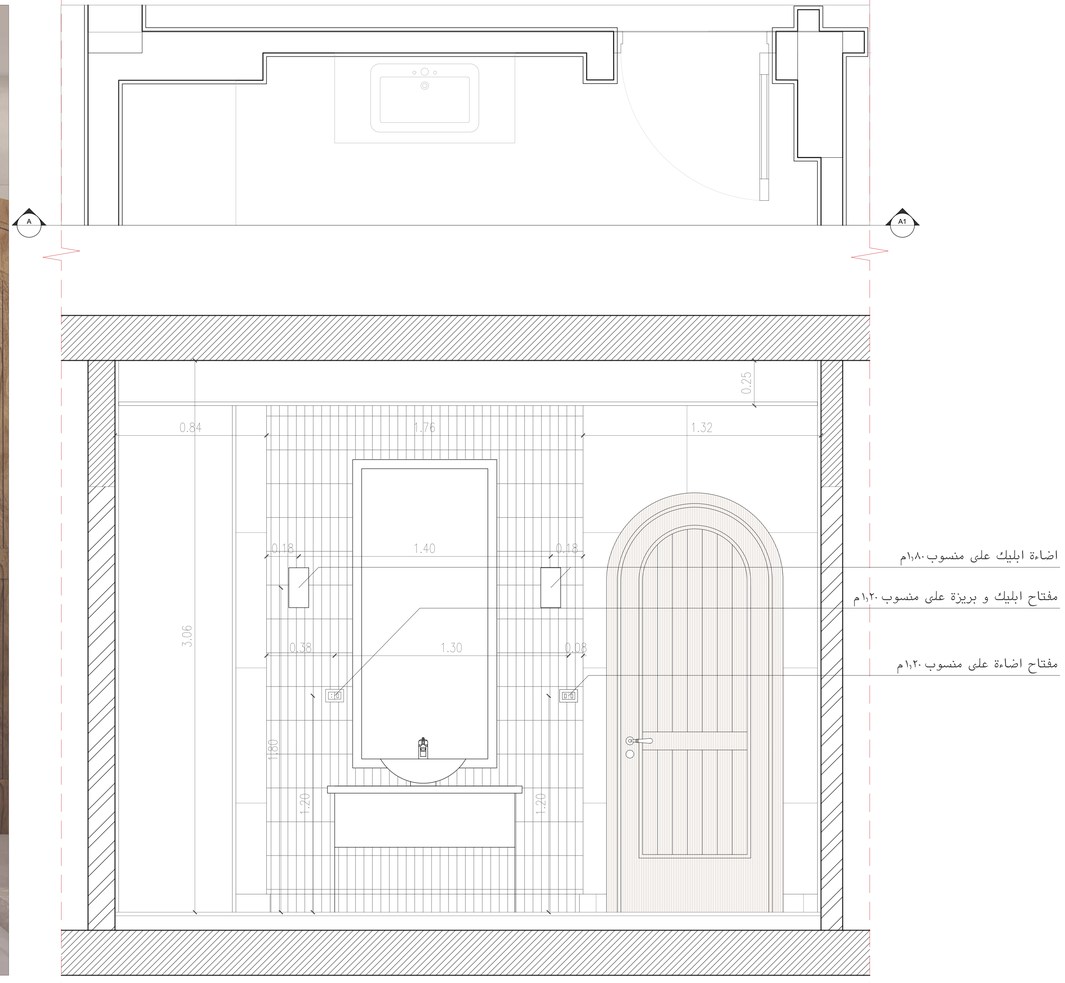

18 INTERNAL ELEVATIONS - FAMILY BATHROOM

مساقط راسية - حمام العائلة

THD STUDIO
www.THDstudio.net

CLIENT:
ا/ ايناس البيلى
MRS. Inas El Beily

TITLE:
فيـــلا سكنيـــة
Residential Villa

LAVISTA DEVELOPMENTS

DRAWING :
INTERNAL ELEVATIONS
مساقط راسية

DATE:	SCALE:	PAPER:
JUN, 2026	1 : 100	A0

DRAWING BY:
ENG. BAHAELDIN AHMED

REVISED BY:
ENG. ZAHRAA SALEH

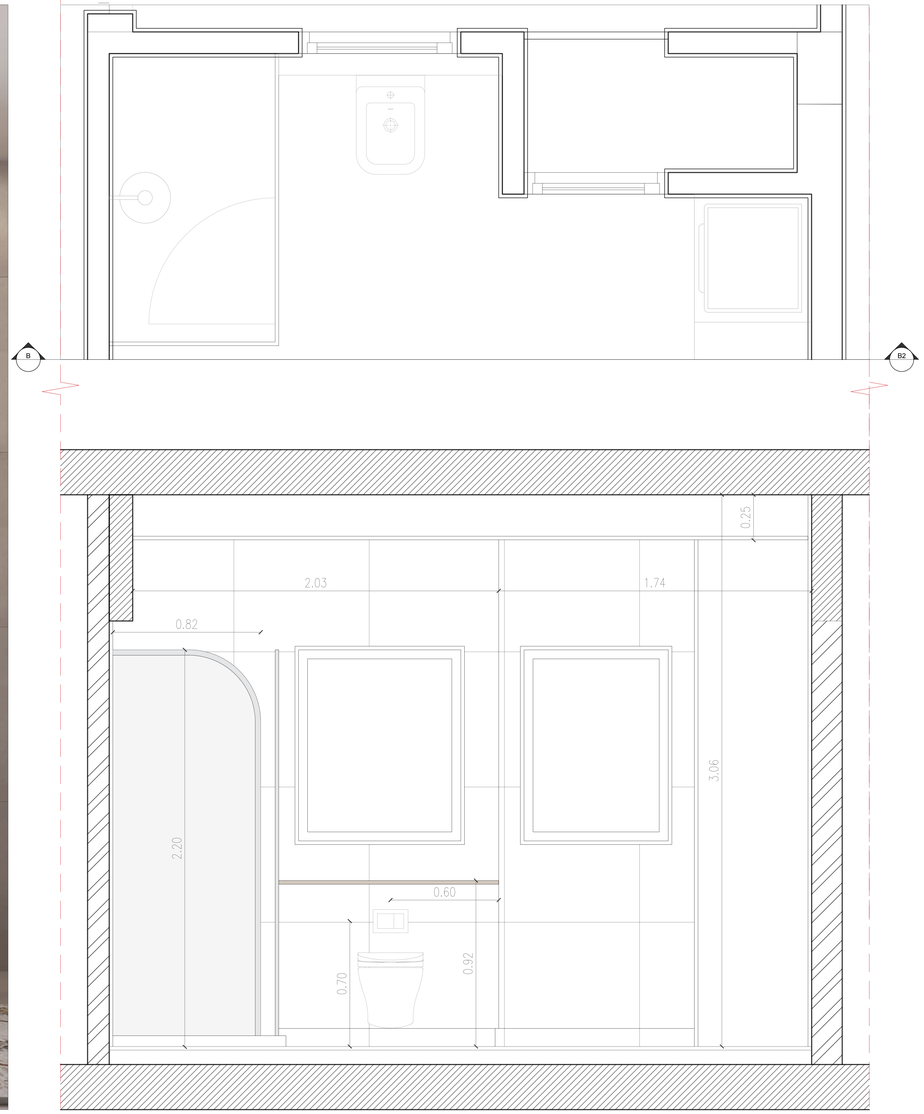

18 INTERNAL ELEVATIONS - FAMILY BATHROOM

مساقط راسية - حمام العائلة

THD
STUDIO
www.THDstudio.net

CLIENT:
ا / ايناس البيلى
MRS. Inas El Beily

TITLE:
فيـــلا سكنيـــة
Residential Villa

LAVISTA DEVELOPMENTS

DRAWING :
INTERNAL ELEVATIONS
مساقط راسية

DATE:	SCALE:	PAPER:
JUN, 2026	1 : 100	A0

DRAWING BY:
ENG. BAHAELDIN AHMED

REVISED BY:
ENG. ZAHRAA SALEH

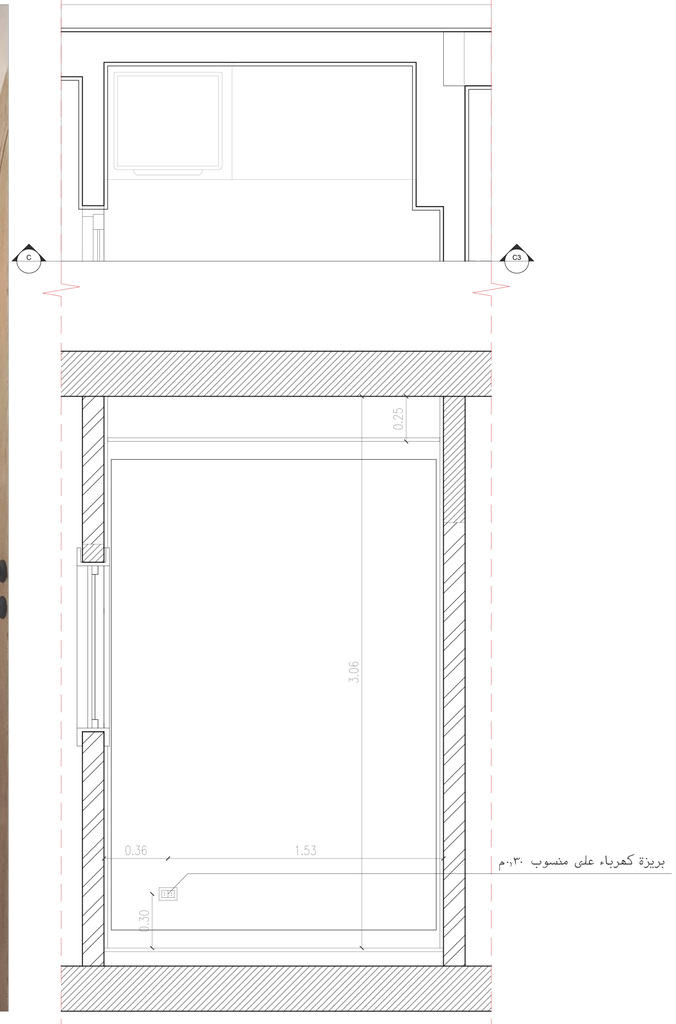

18 INTERNAL ELEVATIONS - FAMILY BATHROOM

مساقط راسية - حمام العائلة

THD
STUDIO
www.THDstudio.net

CLIENT:
ا / ايناس البيلى
MRS. Inas El Beily

TITLE:
فيـــلا سكنيـــة
Residential Villa

LAVISTA DEVELOPMENTS

DRAWING :
INTERNAL ELEVATIONS
مساقط راسية

DATE:	SCALE:	PAPER:
JUN, 2026	1 : 100	A0

DRAWING BY:
ENG. BAHAELDIN AHMED

REVISED BY:
ENG. ZAHRAA SALEH

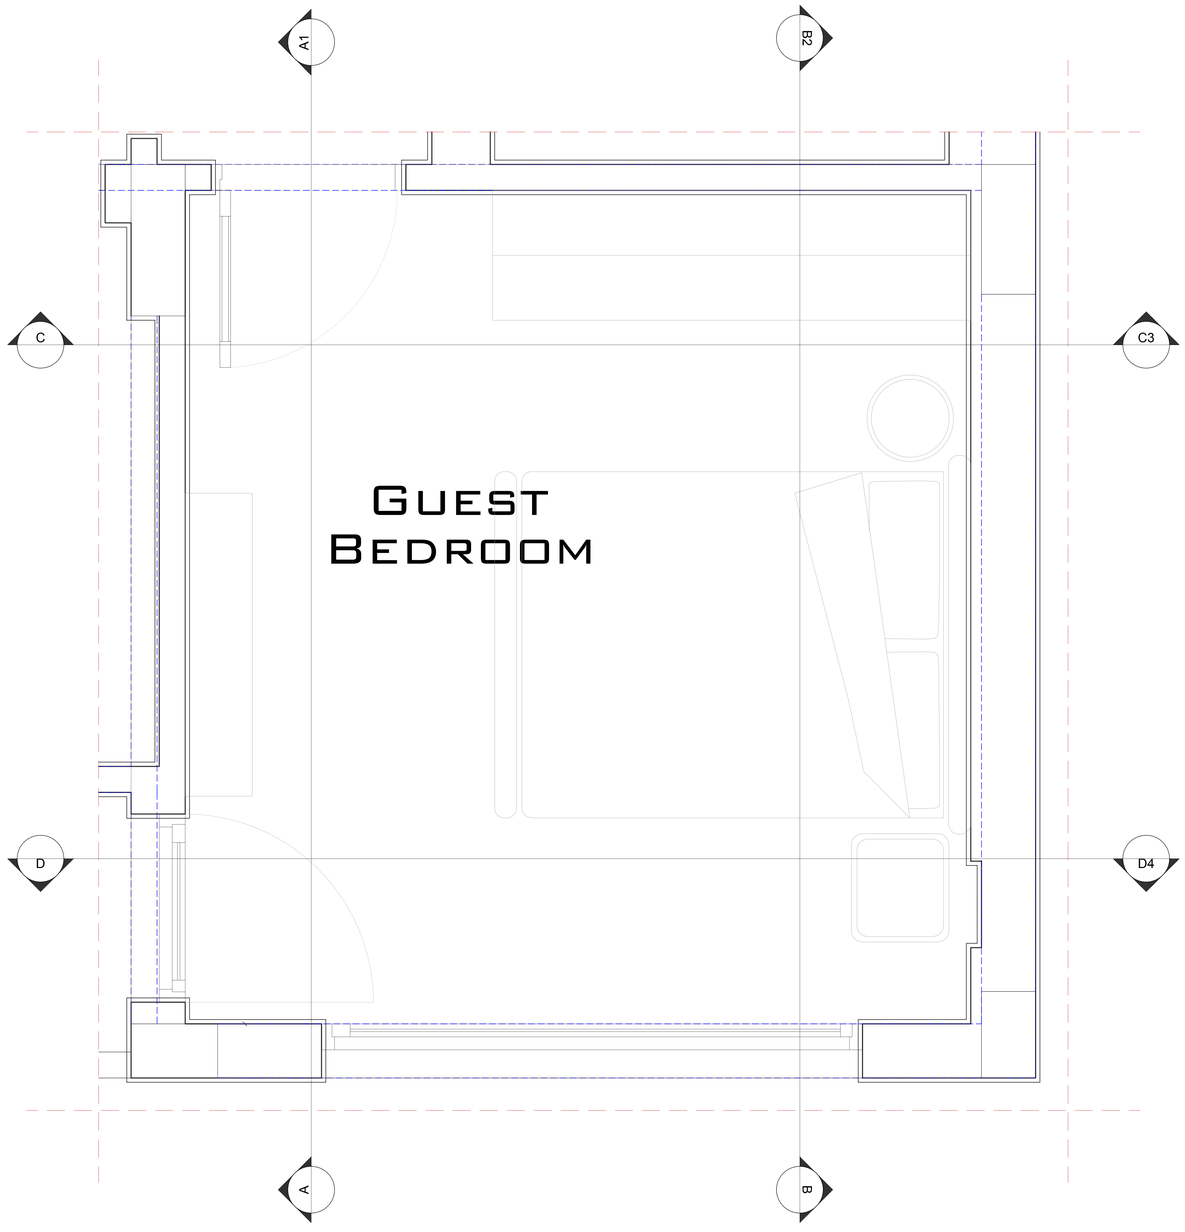

19 GUEST BEDROOM PLAN

مسقط افقى لغرفة الضيوف

THD
STUDIO
www.THDstudio.net

CLIENT:
ا / ايناس البيلى
MRS. Inas El Beily

TITLE:
فيـــلا سكنيـــة
Residential Villa

LAVISTA DEVELOPMENTS

DRAWING :
MASTER SUITE PLAN
مسقط افقى لجناح النوم الرئيسى

DATE:	SCALE:	PAPER:
JUN, 2026	1 : 100	A0

DRAWING BY:
ENG. BAHAELDIN AHMED

REVISED BY:
ENG. ZAHRAA SALEH

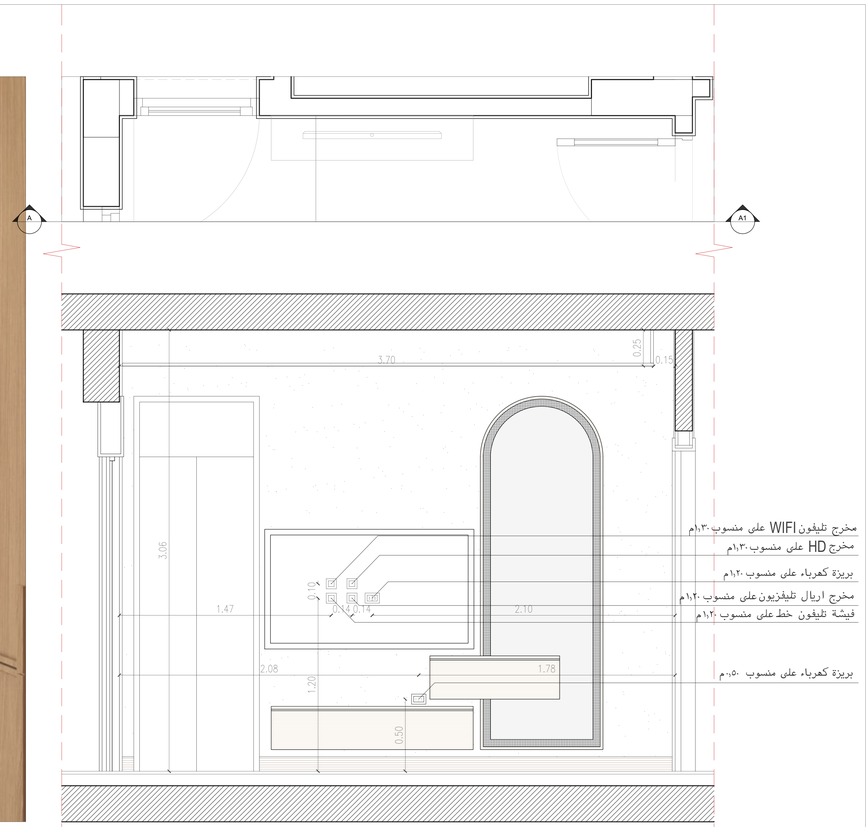

19 INTERNAL ELEVATIONS - GUEST BEDROOM

مساقط راسية - غرفة الضيوف

THD STUDIO
www.THDstudio.net

CLIENT:
ا / ايناس البيلى
MRS. Inas El Beily

TITLE:
فيـــلا سكنيـــة
Residential Villa

LAVISTA DEVELOPMENTS

DRAWING :
INTERNAL ELEVATIONS
مساقط راسية

DATE:	SCALE:	PAPER:
JUN, 2026	1 : 100	A0

DRAWING BY:
ENG. BAHAELDIN AHMED

REVISED BY:
ENG. ZAHRAA SALEH

THD
STUDIO
www.THDstudio.net

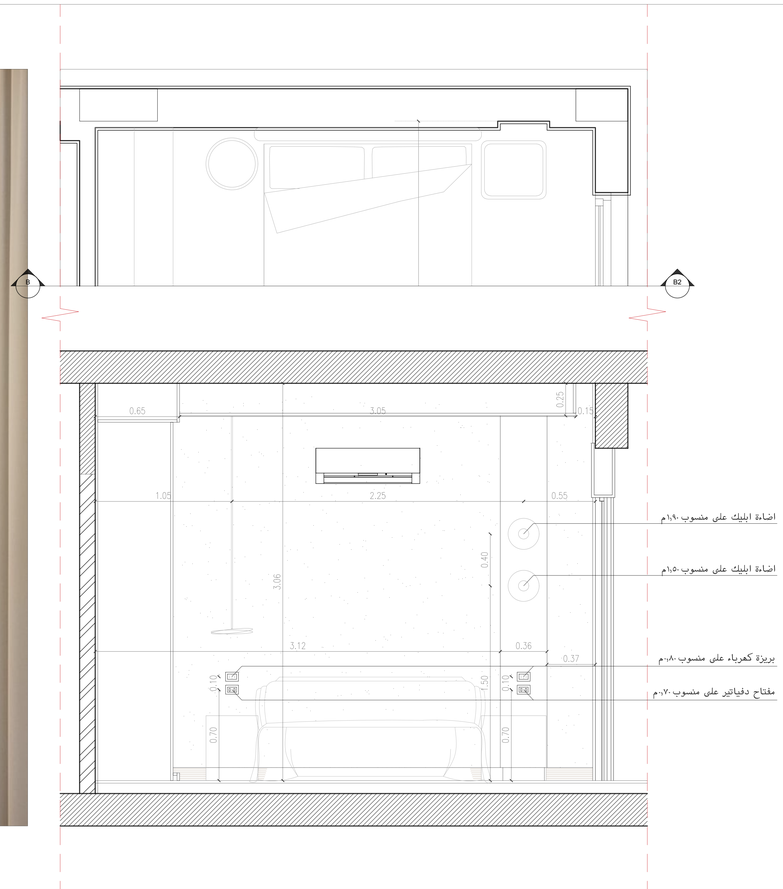

19 INTERNAL ELEVATIONS - GUEST BEDROOM

مساقط راسية - غرفة الضيوف

CLIENT:
ا/ ايناس البيلى
MRS. Inas El Beily

TITLE:
فيـــلا سكنيـــة
Residential Villa

LAVISTA DEVELOPMENTS

DRAWING :
INTERNAL ELEVATIONS
مساقط راسية

DATE:	SCALE:	PAPER:
JUN, 2026	1 : 100	A0

DRAWING BY:
ENG. BAHAELDIN AHMED

REVISED BY:
ENG. ZAHRAA SALEH

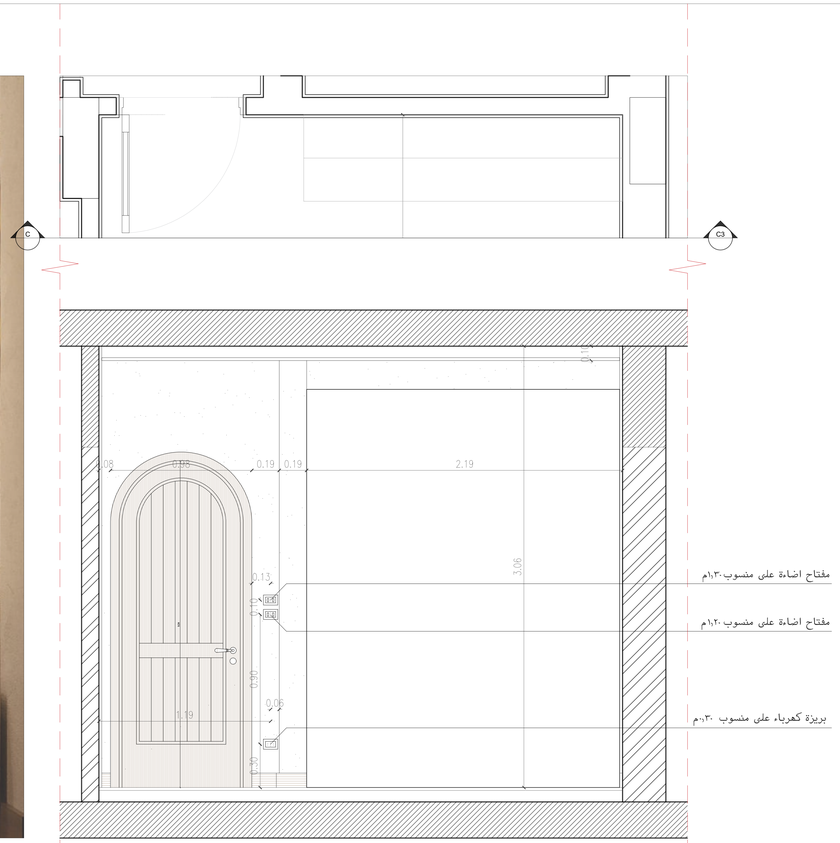

19 INTERNAL ELEVATIONS - GUEST BEDROOM

مساقط راسية - غرفة الضيوف

THD STUDIO
www.THDstudio.net

CLIENT:
ا/ ايناس البيلى
MRS. Inas El Beily

TITLE:
فيـــلا سكنيـــة
Residential Villa

LAVISTA DEVELOPMENTS

DRAWING :
INTERNAL ELEVATIONS
مساقط راسية

DATE:	SCALE:	PAPER:
JUN, 2026	1 : 100	A0

DRAWING BY:
ENG. BAHAELDIN AHMED

REVISED BY:
ENG. ZAHRAA SALEH

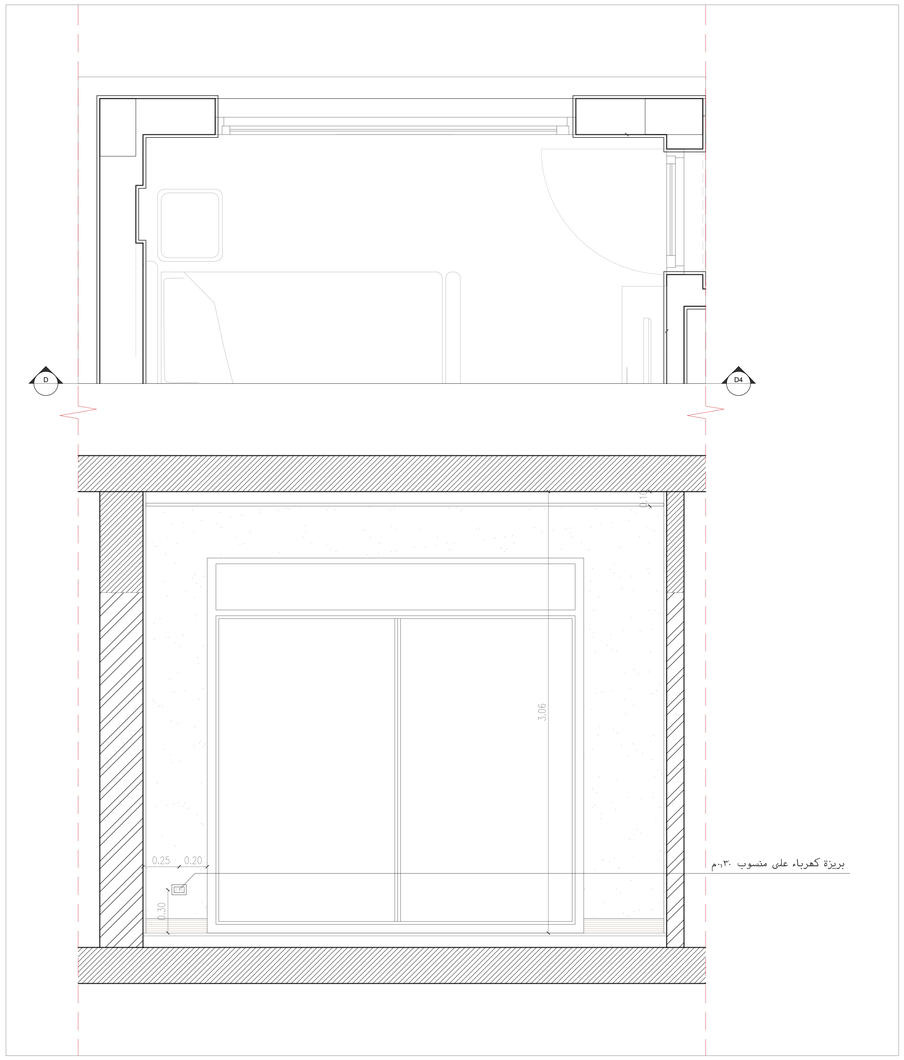

19 INTERNAL ELEVATIONS - GUEST BEDROOM

مساقط راسية - غرفة الضيوف

THD
STUDIO
www.THDstudio.net

CLIENT:
ا / ايناس البيلى
MRS. Inas El Beily

TITLE:
فيـــلا سكنيـــة
Residential Villa

LAVISTA DEVELOPMENTS

DRAWING :
INTERNAL ELEVATIONS
مساقط راسية

DATE:	SCALE:	PAPER:
JUN, 2026	1 : 100	A0

DRAWING BY:
ENG. BAHAELDIN AHMED

REVISED BY:
ENG. ZAHRAA SALEH

20

HOME OFFICE PLAN

مسقط افقى للمكتب

THD
STUDIO
www.THDstudio.net

CLIENT:
ا / ايناس البيلى
MRS. Inas El Beily

TITLE:
فيـــلا سكنيـــة
Residential Villa

LAVISTA DEVELOPMENTS

DRAWING :
INTERNAL ELEVATIONS
مساقط راسية

DATE:	SCALE:	PAPER:
JUN, 2026	1 : 100	A0

DRAWING BY:
ENG. BAHAELDIN AHMED

REVISED BY:
ENG. ZAHRAA SALEH

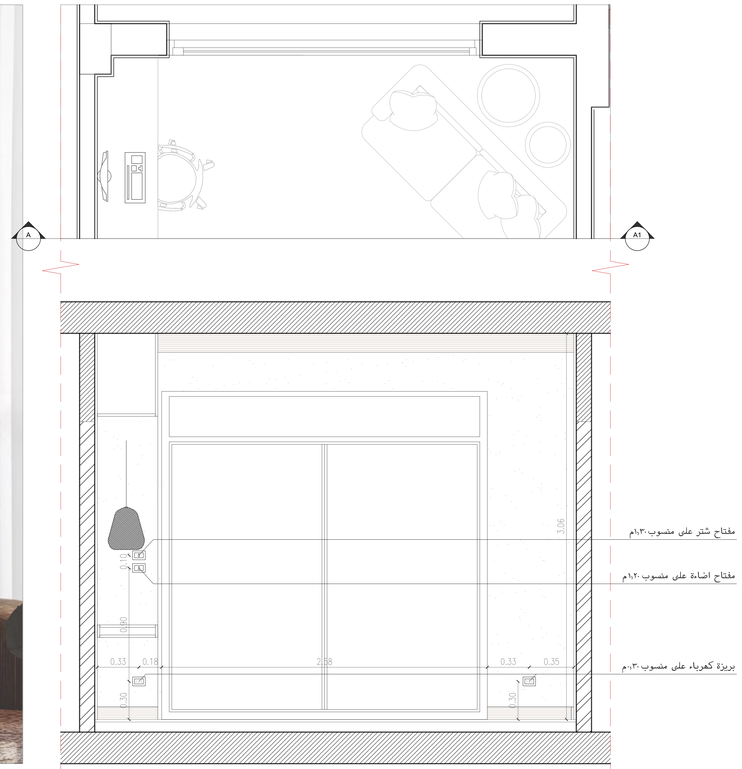

INTERNAL ELEVATIONS - HOME OFFICE

مساقط راسية - المكتب

THD
STUDIO
www.THDstudio.net

CLIENT:
ا/ ايناس البيلى
MRS. Inas El Beily

TITLE:
فيـــلا سكنيـــة
Residential Villa

LAVISTA DEVELOPMENTS

DRAWING :
INTERNAL ELEVATIONS
مساقط راسية

DATE:	SCALE:	PAPER:
JUN, 2026	1 : 100	A0

DRAWING BY:
ENG. BAHAELDIN AHMED

REVISED BY:
ENG. ZAHRAA SALEH

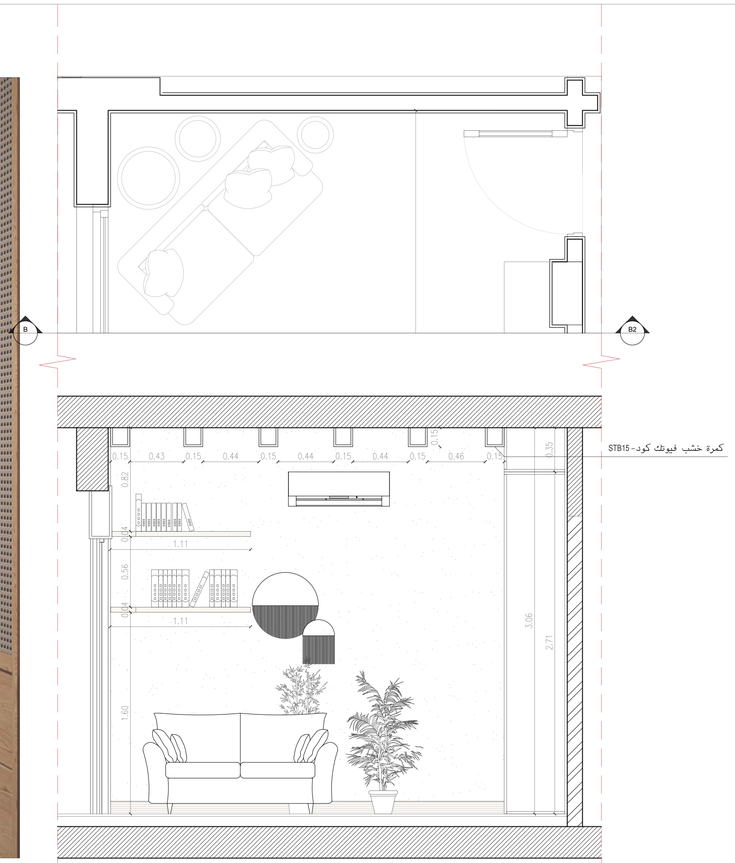

20 INTERNAL ELEVATIONS - HOME OFFICE

مساقط راسية - المكتب

THD STUDIO
www.THDstudio.net

CLIENT:
ا / ايناس البيلى
MRS. Inas El Beily

TITLE:
فيـــلا سكنيـــة
Residential Villa

LAVISTA DEVELOPMENTS

DRAWING :
INTERNAL ELEVATIONS
مساقط راسية

DATE:	SCALE:	PAPER:
JUN, 2026	1 : 100	A0

DRAWING BY:
ENG. BAHAELDIN AHMED

REVISED BY:
ENG. ZAHRAA SALEH

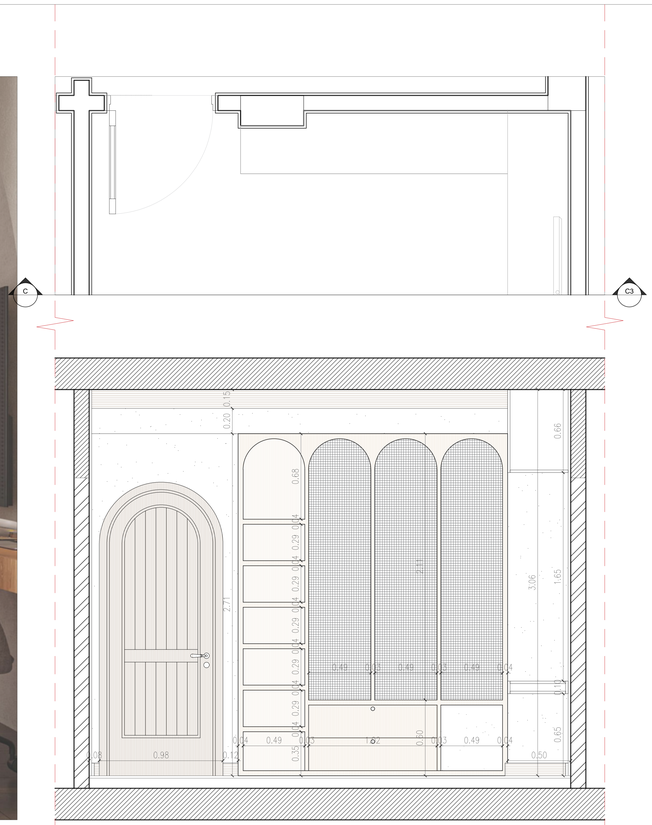

INTERNAL ELEVATIONS - HOME OFFICE

مساقط راسية - المكتب

THD
STUDIO
www.THDstudio.net

CLIENT:
ا / ايناس البيلى
MRS. Inas El Beily

TITLE:
فيـــلا سكنيـــة
Residential Villa

LAVISTA DEVELOPMENTS

DRAWING :
INTERNAL ELEVATIONS
مساقط راسية

DATE:	SCALE:	PAPER:
JUN, 2026	1 : 100	A0

DRAWING BY:
ENG. BAHAELDIN AHMED

REVISED BY:
ENG. ZAHRAA SALEH

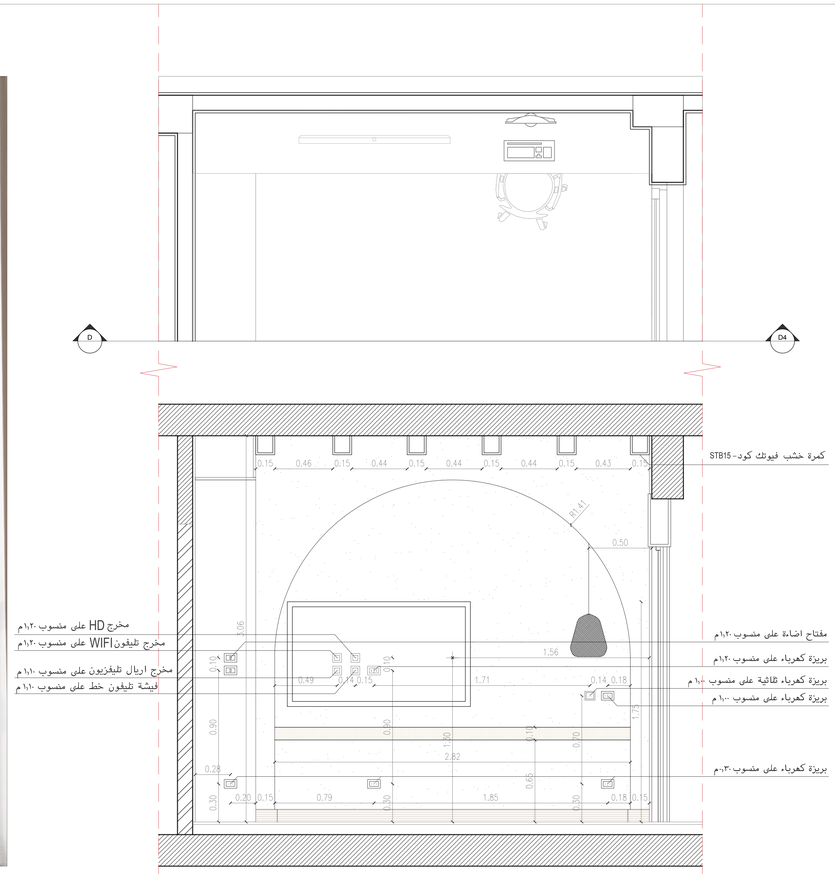

INTERNAL ELEVATIONS - HOME OFFICE

مساقط راسية - المكتب

THD STUDIO
www.THDstudio.net

CLIENT:
ا / ايناس البيلى
MRS. Inas El Beily

TITLE:
فيـــلا سكنيـــة
Residential Villa

LAVISTA DEVELOPMENTS

DRAWING :
INTERNAL ELEVATIONS
مساقط راسية

DATE:	SCALE:	PAPER:
JUN, 2026	1 : 100	A0

DRAWING BY:
ENG. BAHAELDIN AHMED

REVISED BY:
ENG. ZAHRAA SALEH

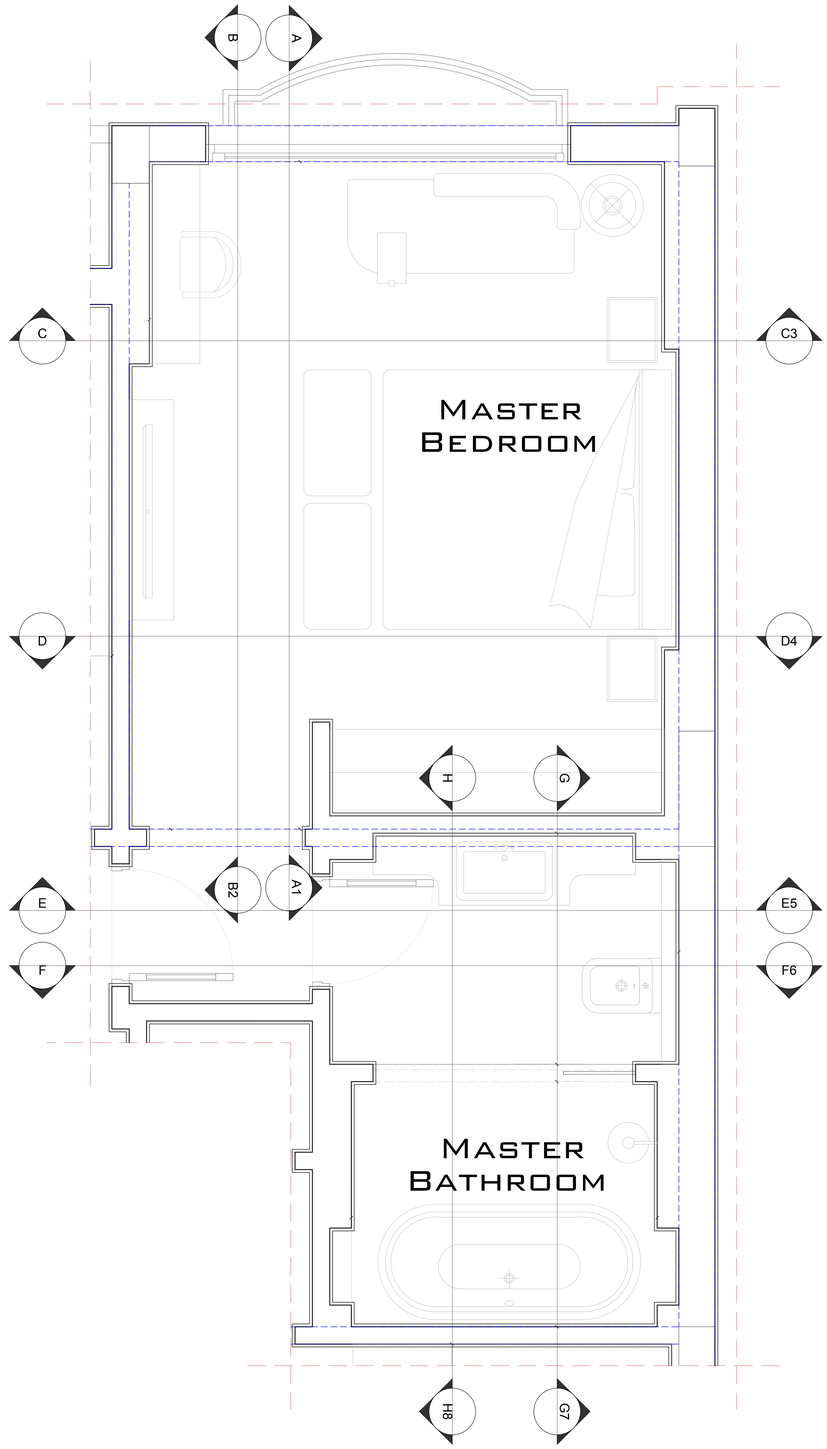

21

MASTER SUITE PLAN

مسقط افقى لجناح النوم الرئيسى

THD
STUDIO
www.THDstudio.net

CLIENT:
ا / ايناس البيلى
MRS. Inas El Beily

TITLE:
فيـــلا سكنيـــة
Residential Villa

LAVISTA
DEVELOPMENTS

DRAWING :
MASTER SUITE PLAN
مسقط افقى لجناح النوم الرئيسى

DATE:	SCALE:	PAPER:
JUN, 2026	1 : 100	A0

DRAWING BY:
ENG. BAHAELDIN AHMED

REVISED BY:
ENG. ZAHRAA SALEH

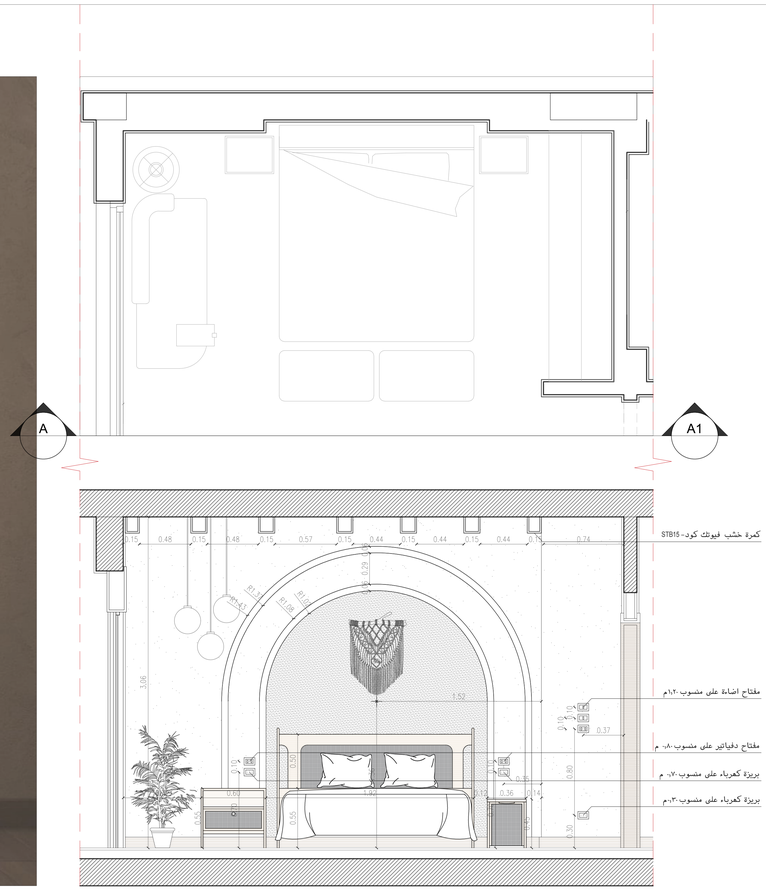

21 INTERNAL ELEVATIONS - MASTER BEDROOM

مساقط راسية - غرفة النوم الرئيسية

THD STUDIO
www.THDstudio.net

CLIENT:
ا/ ايناس البيلى
MRS. Inas El Beily

TITLE:
فيـــلا سكنيـــة
Residential Villa

LAVISTA DEVELOPMENTS

DRAWING :
INTERNAL ELEVATIONS
مساقط راسية

DATE:	SCALE:	PAPER:
JUN, 2026	1 : 100	A0

DRAWING BY:
ENG. BAHAELDIN AHMED

REVISED BY:
ENG. ZAHRAA SALEH

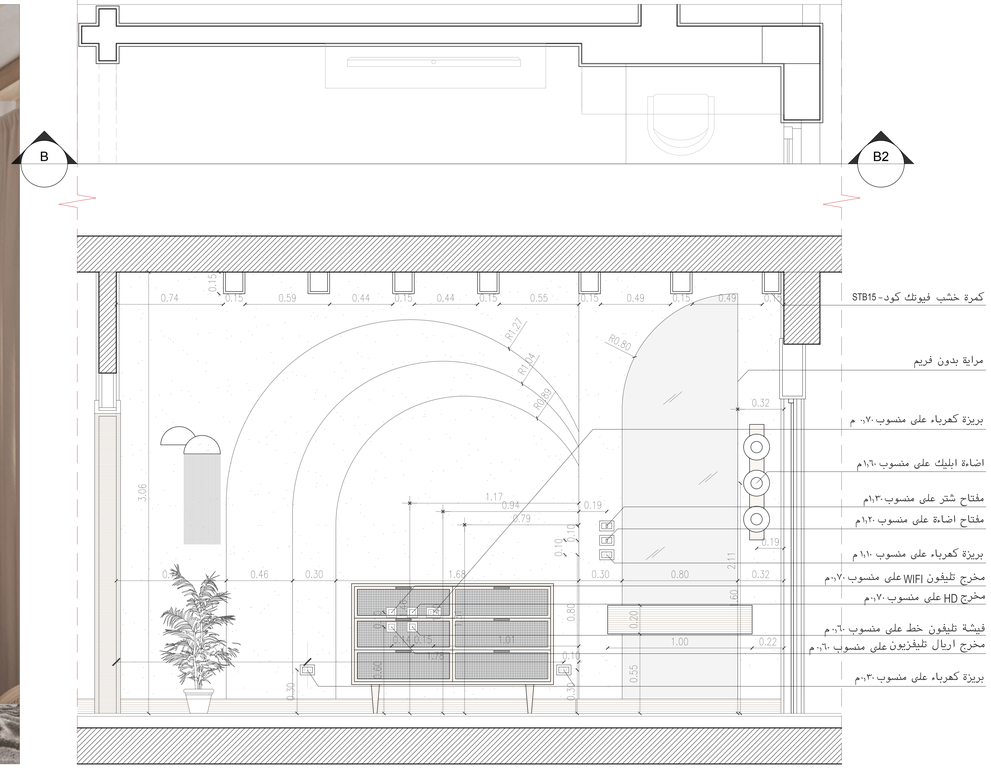

21 INTERNAL ELEVATIONS - MASTER BEDROOM

مساقط راسية - غرفة النوم الرئيسية

THD STUDIO
www.THDstudio.net

CLIENT:
ا/ ايناس البيلى
MRS. Inas El Beily

TITLE:
فيـــلا سكنيـــة
Residential Villa

LAVISTA DEVELOPMENTS

DRAWING :
INTERNAL ELEVATIONS
مساقط راسية

DATE:	SCALE:	PAPER:
JUN, 2026	1 : 100	A0

DRAWING BY:
ENG. BAHAELDIN AHMED

REVISED BY:
ENG. ZAHRAA SALEH

THD
STUDIO
www.THDstudio.net

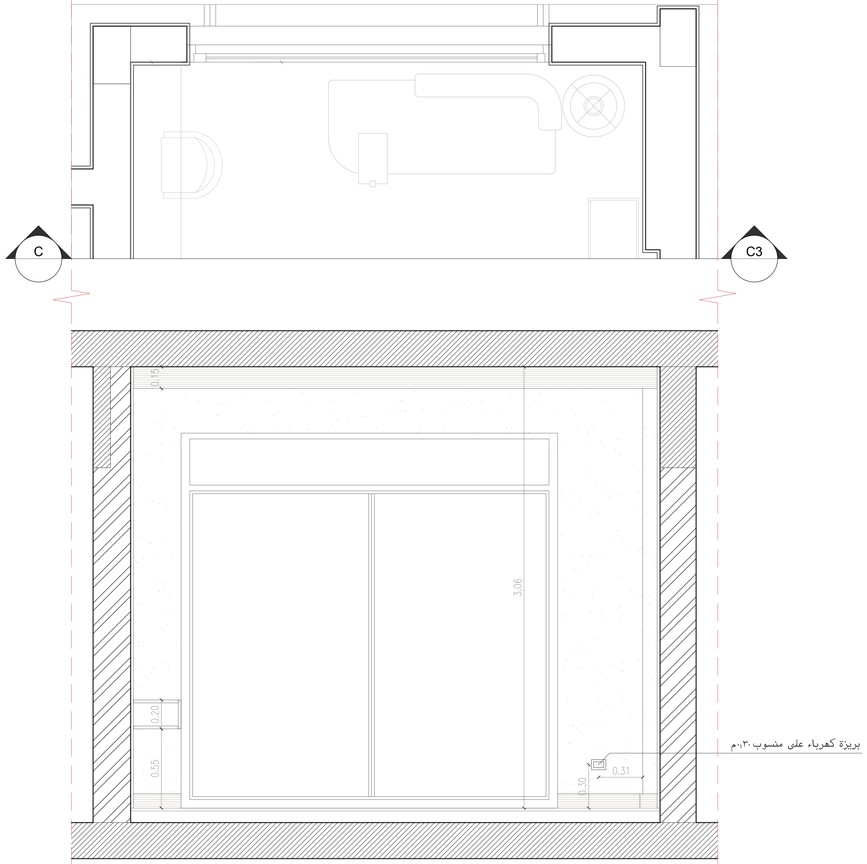

21 INTERNAL ELEVATIONS - MASTER BEDROOM

مساقط راسية - غرفة النوم الرئيسية

CLIENT:
ا/ ايناس البيلى
MRS. Inas El Beily

TITLE:
فيـــلا سكنيـــة
Residential Villa

LAVISTA DEVELOPMENTS

DRAWING :
INTERNAL ELEVATIONS
مساقط راسية

DATE:	SCALE:	PAPER:
JUN, 2026	1 : 100	A0

DRAWING BY:
ENG. BAHAELDIN AHMED

REVISED BY:
ENG. ZAHRAA SALEH

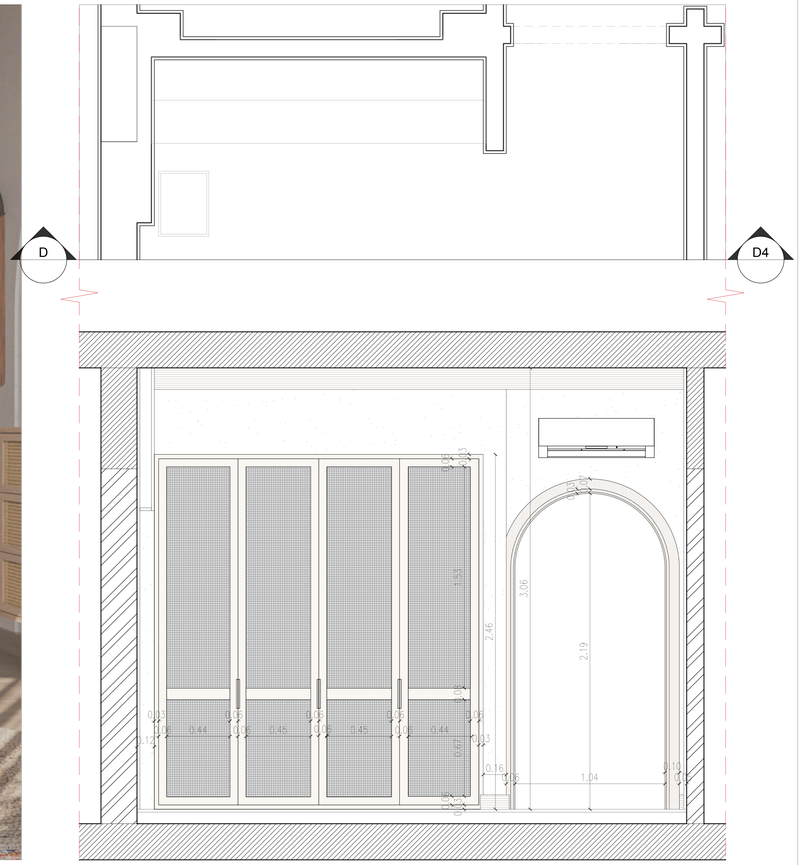

21 INTERNAL ELEVATIONS - MASTER BEDROOM

مساقط راسية - غرفة النوم الرئيسية

THD STUDIO
www.THDstudio.net

CLIENT:
ا/ ايناس البيلى
MRS. Inas El Beily

TITLE:
فيـــلا سكنيـة
Residential Villa

LAVISTA DEVELOPMENTS

DRAWING :
INTERNAL ELEVATIONS
مساقط راسية

DATE:	SCALE:	PAPER:
JUN, 2026	1 : 100	A0

DRAWING BY:
ENG. BAHAELDIN AHMED

REVISED BY:
ENG. ZAHRAA SALEH

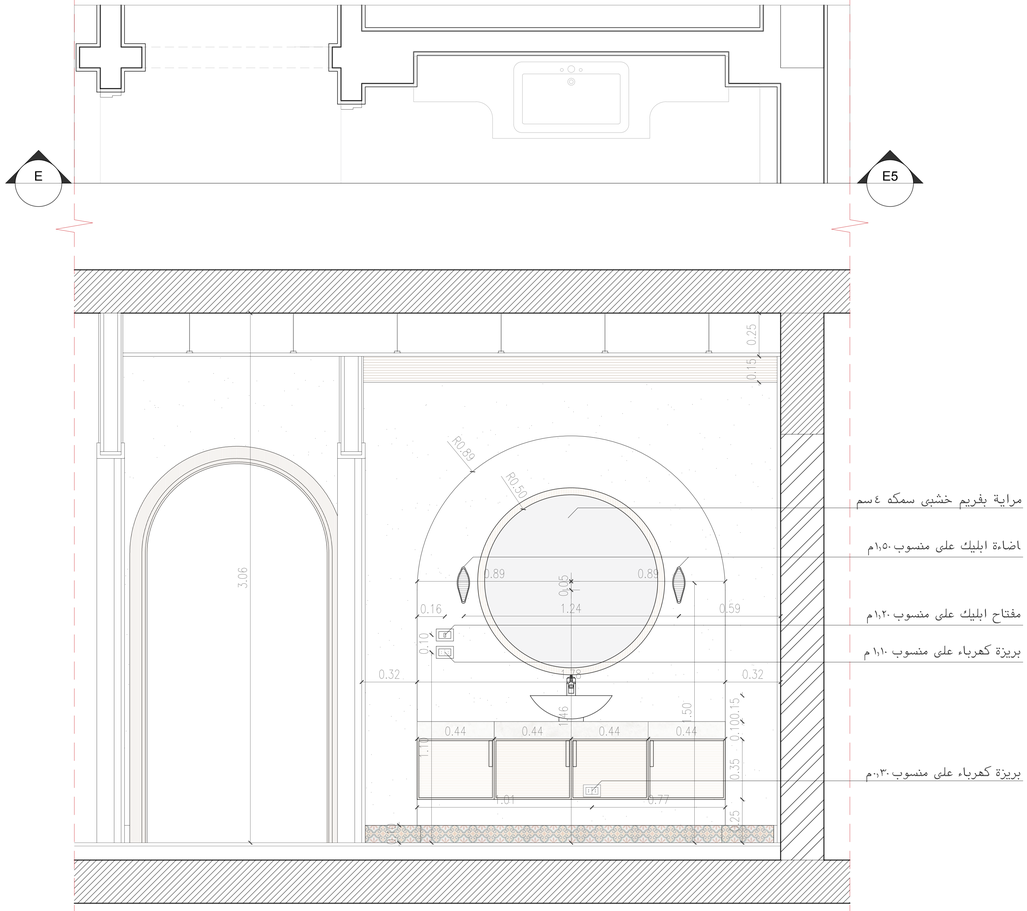

21 INTERNAL ELEVATIONS - MASTER BATHROOM

مساقط راسية - حمام الجناح الرئيسى

THD
STUDIO
www.THDstudio.net

CLIENT:
ا / ايناس البيلى
MRS. Inas El Beily

TITLE:
فيـــلا سكنيـــة
Residential Villa

LAVISTA DEVELOPMENTS

DRAWING :
INTERNAL ELEVATIONS
مساقط راسية

DATE:	SCALE:	PAPER:
JUN, 2026	1 : 100	A0

DRAWING BY:
ENG. BAHAELDIN AHMED

REVISED BY:
ENG. ZAHRAA SALEH

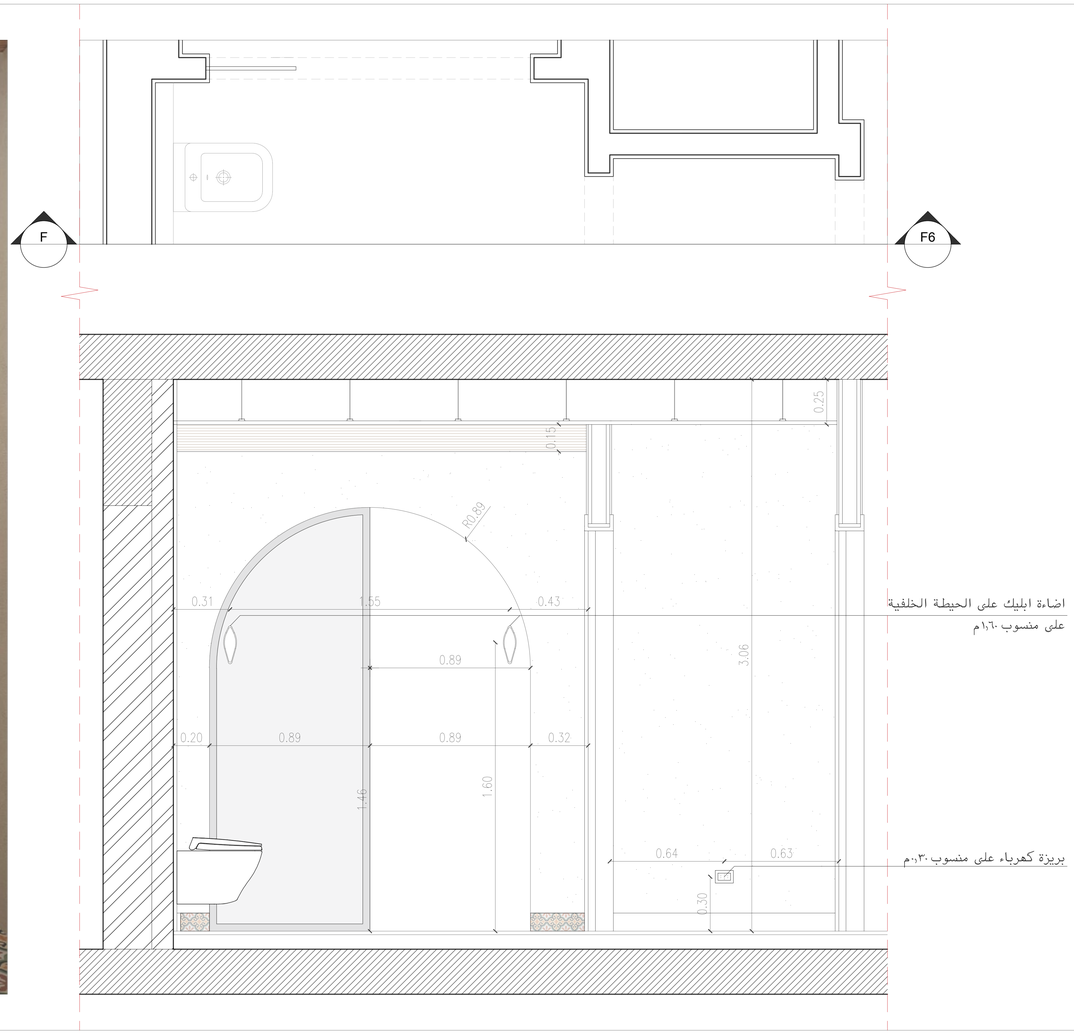

21 INTERNAL ELEVATIONS - MASTER BATHROOM

مساقط راسية - حمام الجناح الرئيسى

THD STUDIO
www.THDstudio.net

CLIENT:
ا / ايناس البيلى
MRS. Inas El Beily

TITLE:
فيـــلا سكنيـــة
Residential Villa

LAVISTA DEVELOPMENTS

DRAWING :
INTERNAL ELEVATIONS
مساقط راسية

DATE:	SCALE:	PAPER:
JUN, 2026	1 : 100	A0

DRAWING BY:
ENG. BAHAELDIN AHMED

REVISED BY:
ENG. ZAHRAA SALEH

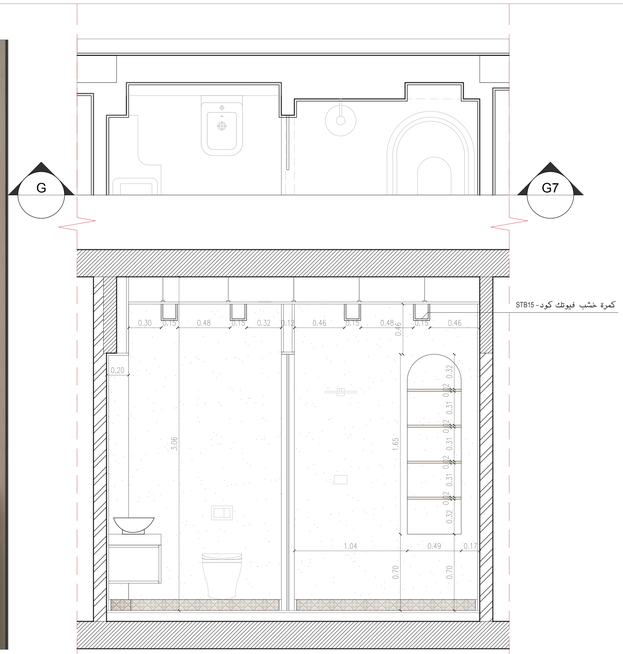

21 INTERNAL ELEVATIONS - MASTER BATHROOM

مساقط راسية - حمام الجناح الرئيسى

THD
STUDIO
www.THDstudio.net

CLIENT:
ا/ ايناس البيلى
MRS. Inas El Beily

TITLE:
فيـــلا سكنيـــة
Residential Villa

LAVISTA DEVELOPMENTS

DRAWING :
INTERNAL ELEVATIONS
مساقط راسية

DATE:	SCALE:	PAPER:
JUN, 2026	1 : 100	A0

DRAWING BY:
ENG. BAHAELDIN AHMED

REVISED BY:
ENG. ZAHRAA SALEH

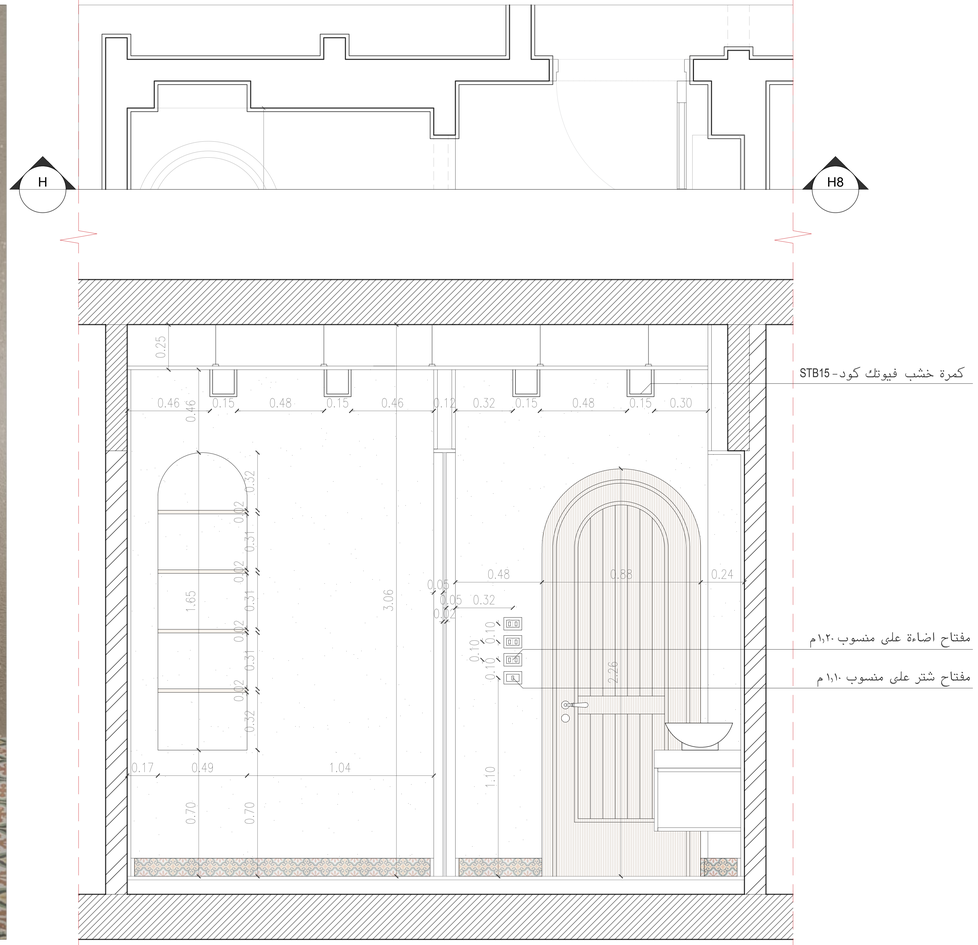

21 INTERNAL ELEVATIONS - MASTER BATHROOM

مساقط راسية - حمام الجناح الرئيسى

THD STUDIO
www.THDstudio.net

CLIENT:
ا / ايناس البيلى
MRS. Inas El Beily

TITLE:
فيـــلا سكنيـــة
Residential Villa

LAVISTA DEVELOPMENTS

DRAWING :
INTERNAL ELEVATIONS
مساقط راسية

DATE:	SCALE:	PAPER:
JUN, 2026	1 : 100	A0

DRAWING BY:
ENG. BAHAELDIN AHMED

REVISED BY:
ENG. ZAHRAA SALEH

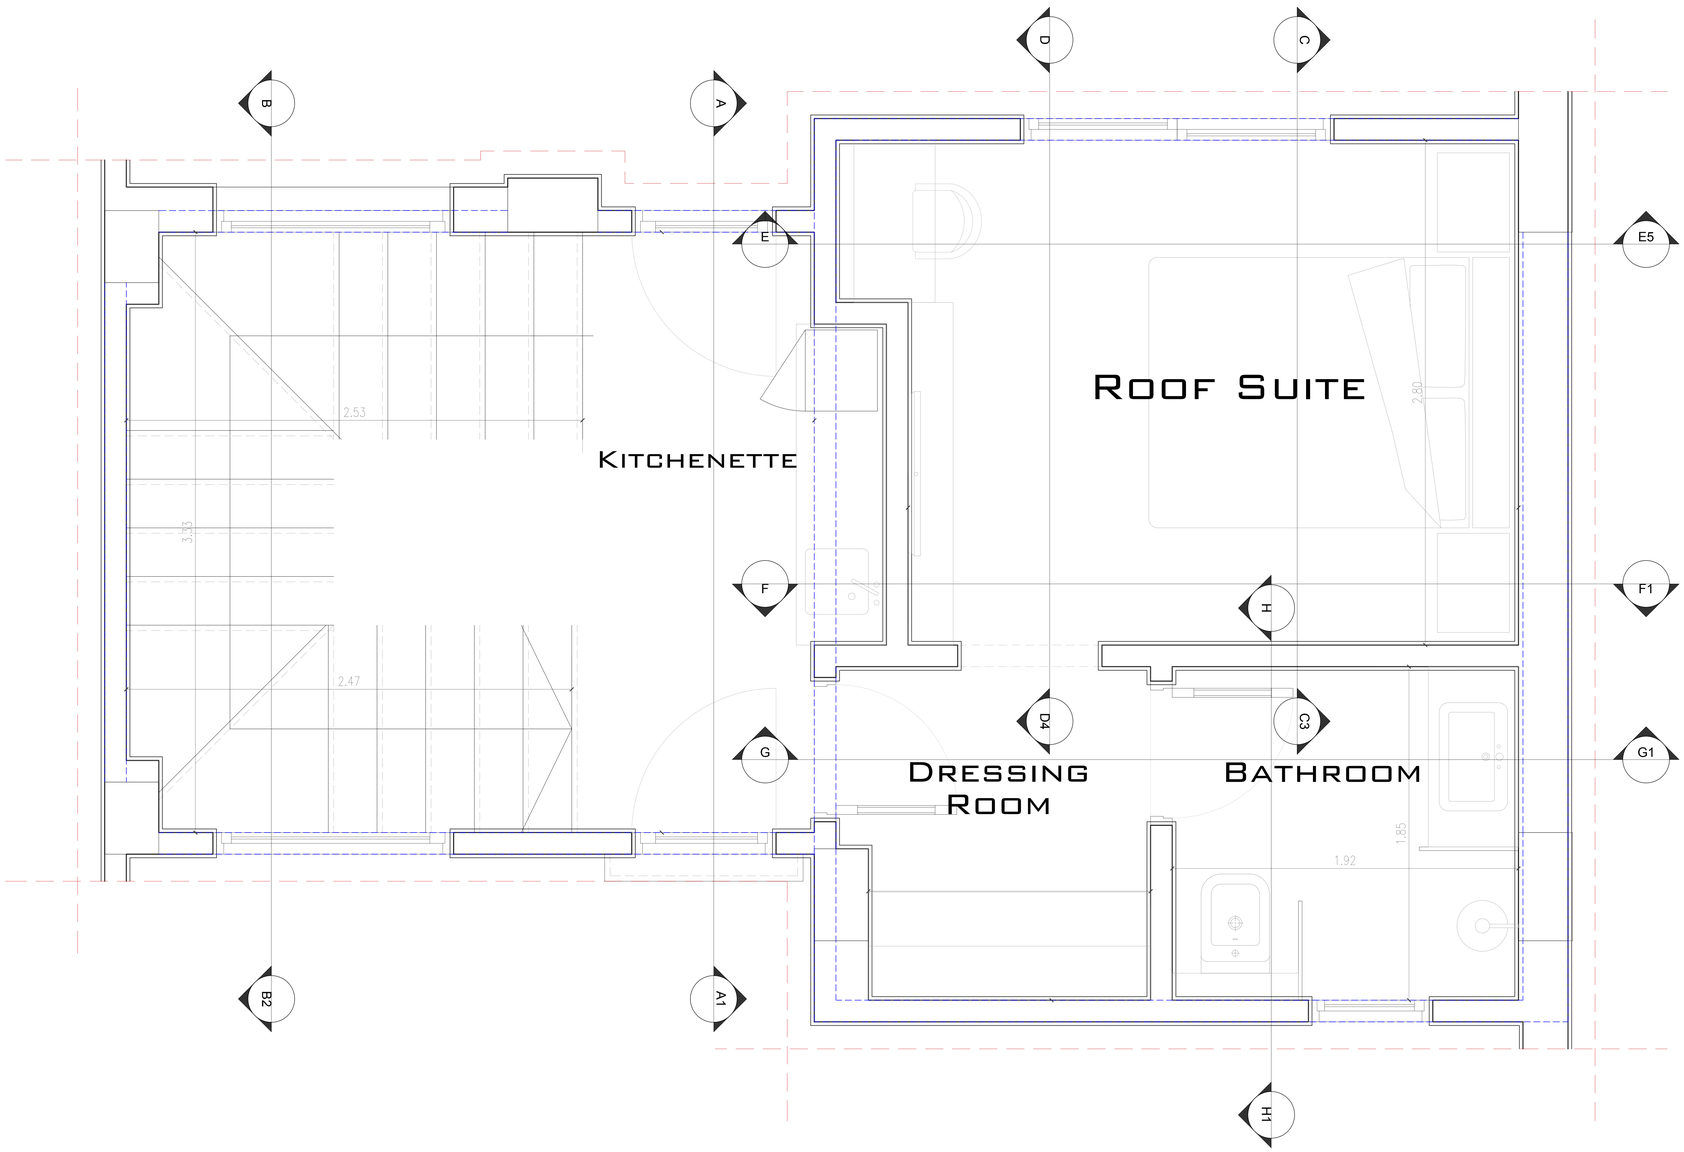

22 ROOF FLOOR PLAN

مسقط افقى لدور الروف

THD STUDIO
www.THDstudio.net

CLIENT:
ا / ايناس البيلى
MRS. Inas El Beily

TITLE:
فيـــلا سكنيـــة
Residential Villa

LAVISTA DEVELOPMENTS

DRAWING :
ROOF FLOOR PLAN
مسقط افقى لدور الروف

DATE:	SCALE:	PAPER:
JUN, 2026	1 : 100	A0

DRAWING BY:
ENG. BAHAELDIN AHMED

REVISED BY:
ENG. ZAHRAA SALEH

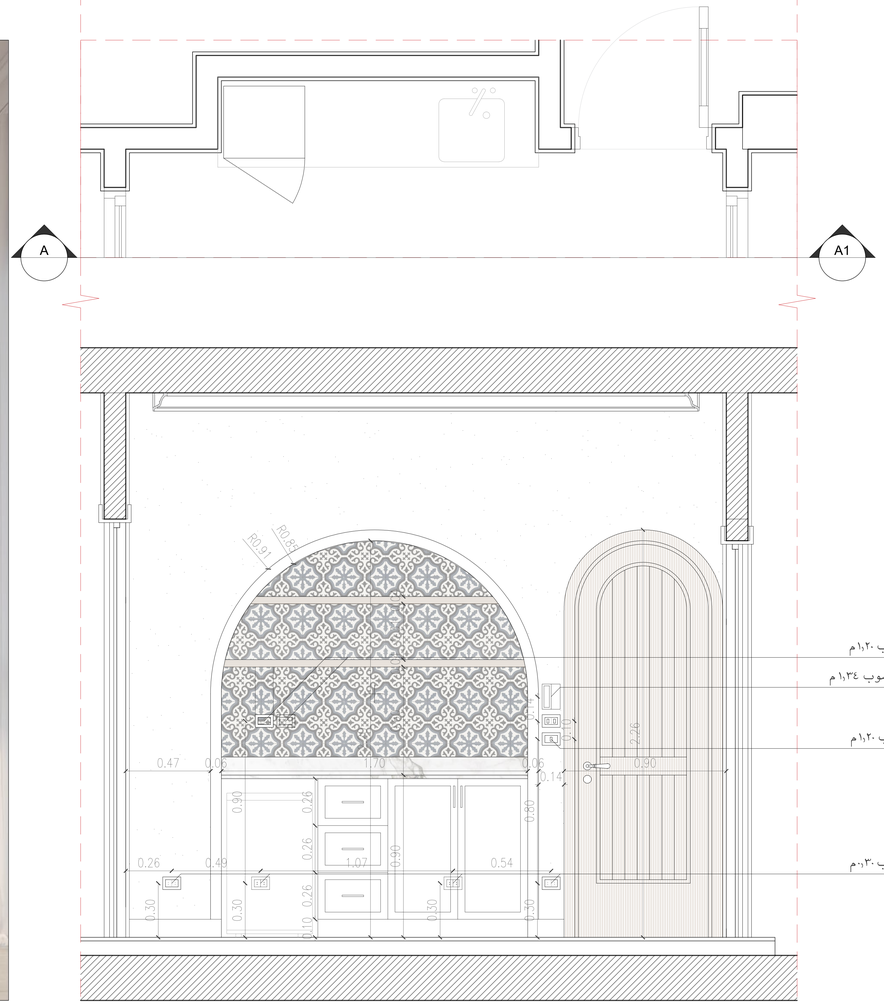

22 INTERNAL ELEVATIONS - ROOF LOBBY

مساقط راسية - لوبى الروف

THD
STUDIO
www.THDstudio.net

CLIENT:
ا / ايناس البيلى
MRS. Inas El Beily

TITLE:
فيـــلا سكنيـــة
Residential Villa

LAVISTA DEVELOPMENTS

DRAWING :
INTERNAL ELEVATIONS
مساقط راسية

DATE:	SCALE:	PAPER:
JUN, 2026	1 : 100	A0

DRAWING BY:
ENG. BAHAELDIN AHMED

REVISED BY:
ENG. ZAHRAA SALEH

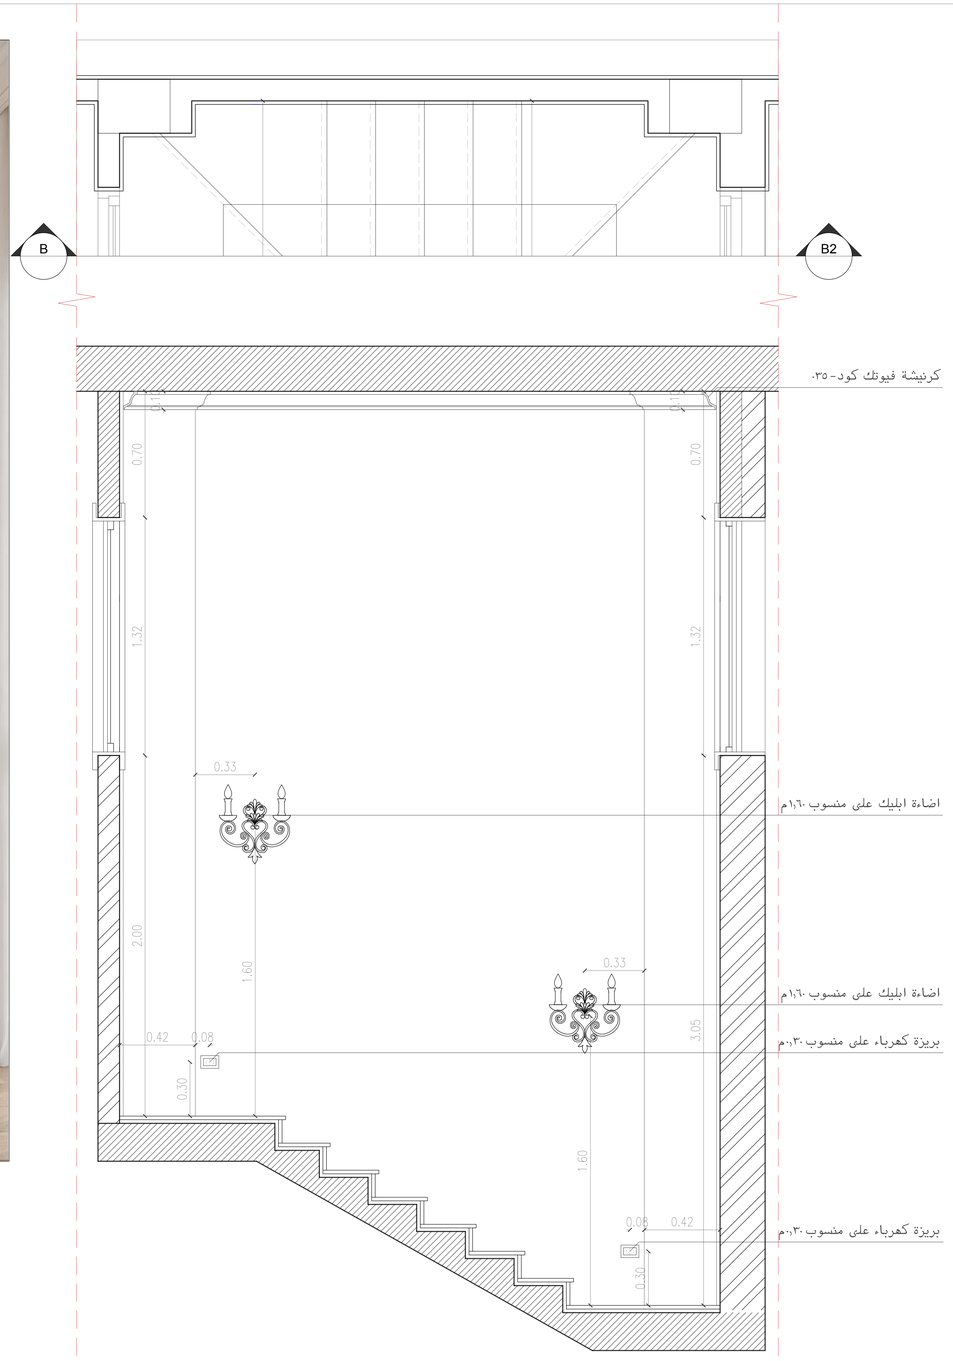

22 INTERNAL ELEVATIONS - ROOF LOBBY

مساقط راسية - لوبى الروف

THD STUDIO
www.THDstudio.net

CLIENT:
ا / ايناس البيلى
MRS. Inas El Beily

TITLE:
فيـــلا سكنيـــة
Residential Villa

LAVISTA DEVELOPMENTS

DRAWING :
INTERNAL ELEVATIONS
مساقط راسية

DATE:	SCALE:	PAPER:
JUN, 2026	1 : 100	A0

DRAWING BY:
ENG. BAHAELDIN AHMED

REVISED BY:
ENG. ZAHRAA SALEH

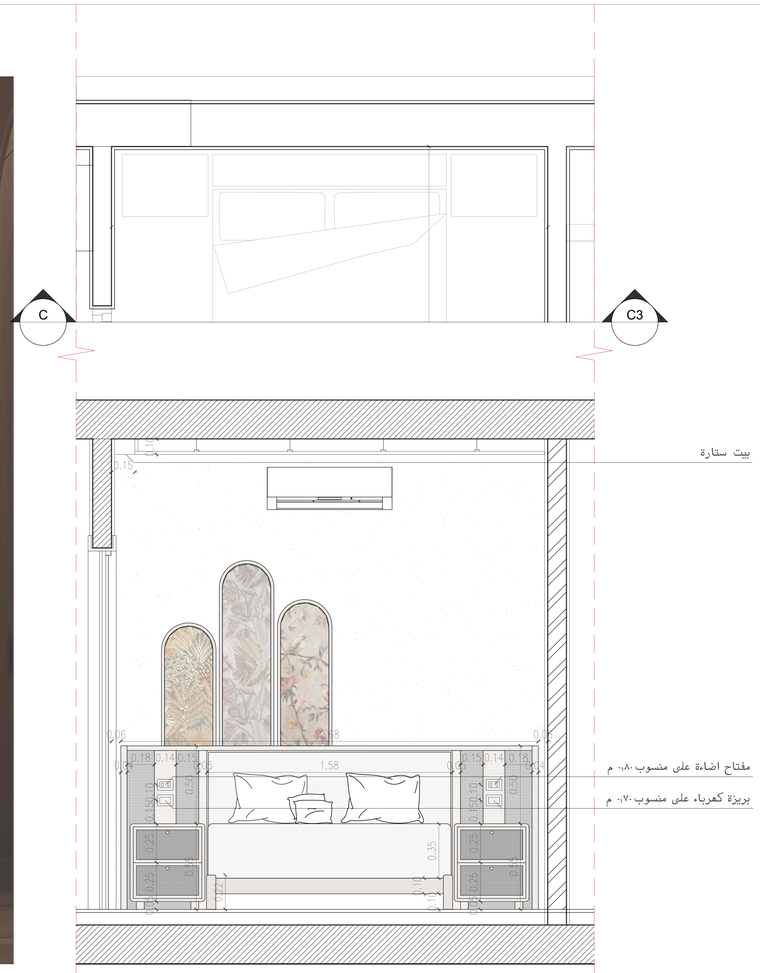

22 INTERNAL ELEVATIONS - Roof Suite

مساقط راسية - غرفة الروف

THD STUDIO
www.THDstudio.net

CLIENT:
ا / ايناس البيلى
MRS. Inas El Beily

TITLE:
فيـــلا سكنيـــة
Residential Villa

LAVISTA DEVELOPMENTS

DRAWING :
INTERNAL ELEVATIONS
مساقط راسية

DATE:	SCALE:	PAPER:
JUN, 2026	1 : 100	A0

DRAWING BY:
ENG. BAHAELDIN AHMED

REVISED BY:
ENG. ZAHRAA SALEH

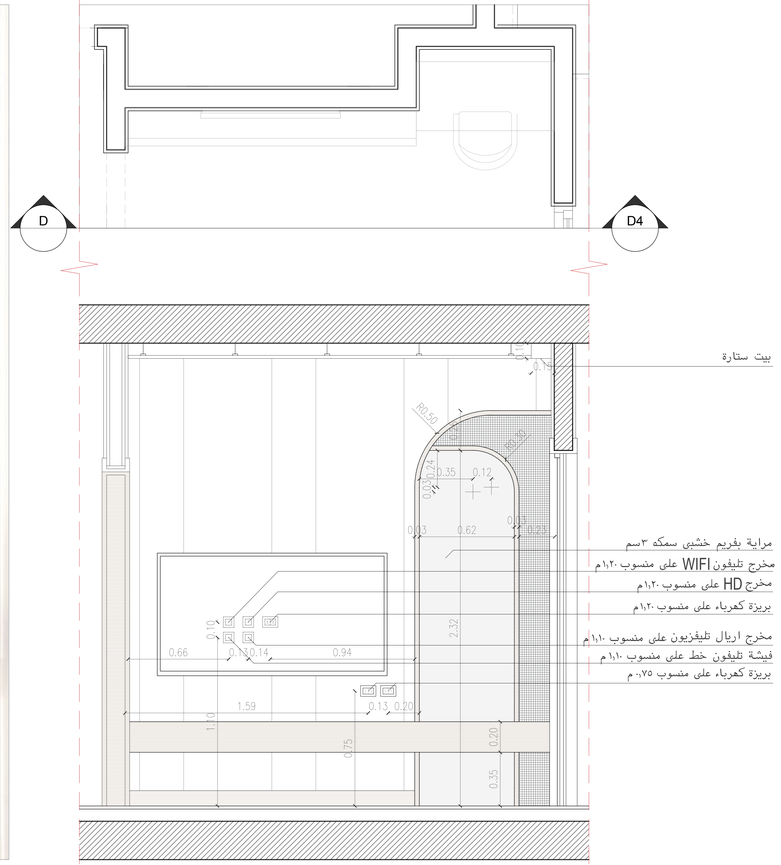

22 INTERNAL ELEVATIONS - Roof Suite

مساقط راسية - غرفة الروف

THD STUDIO
www.THDstudio.net

CLIENT:
ا / ايناس البيلى
MRS. Inas El Beily

TITLE:
فيـــلا سكنيـــة
Residential Villa

LAVISTA DEVELOPMENTS

DRAWING :
INTERNAL ELEVATIONS
مساقط راسية

DATE:	SCALE:	PAPER:
JUN, 2026	1 : 100	A0

DRAWING BY:
ENG. BAHAELDIN AHMED

REVISED BY:
ENG. ZAHRAA SALEH

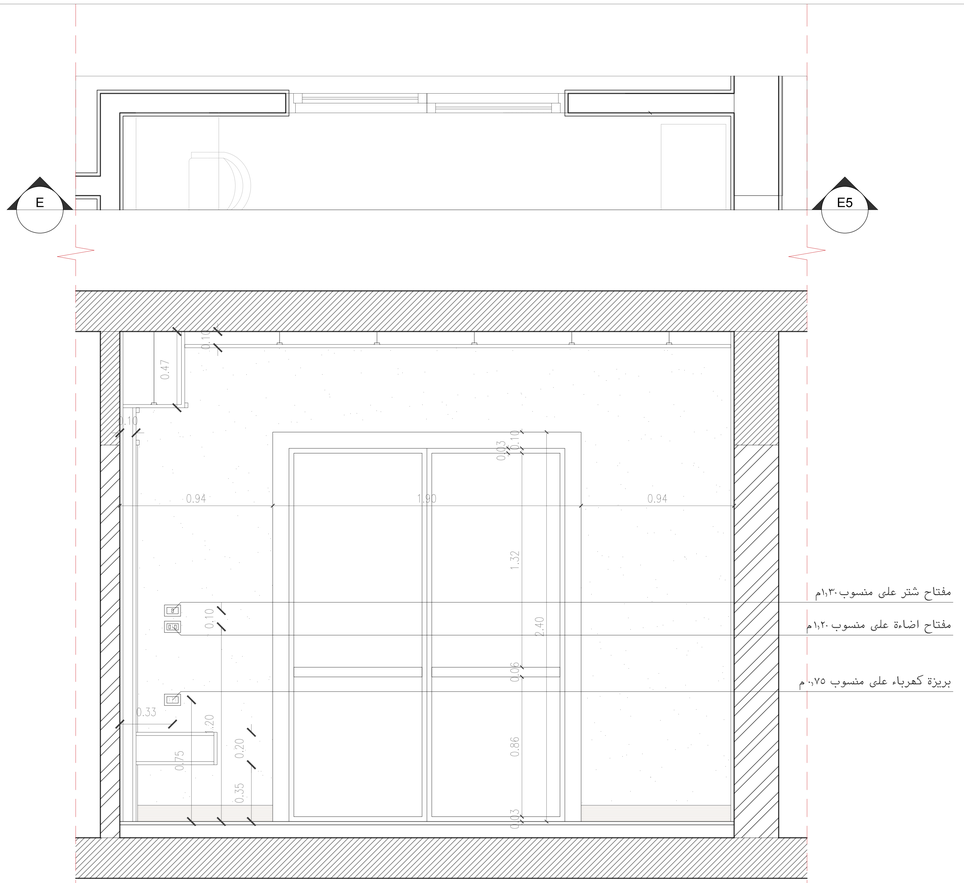

22 INTERNAL ELEVATIONS - Roof Suite

مساقط راسية - غرفة الروف

THD STUDIO
www.THDstudio.net

CLIENT:
ا/ ايناس البيلى
MRS. Inas El Beily

TITLE:
فيـــلا سكنيـــة
Residential Villa

LAVISTA DEVELOPMENTS

DRAWING :
INTERNAL ELEVATIONS
مساقط راسية

DATE:	SCALE:	PAPER:
JUN, 2026	1 : 100	A0

DRAWING BY:
ENG. BAHAELDIN AHMED

REVISED BY:
ENG. ZAHRAA SALEH

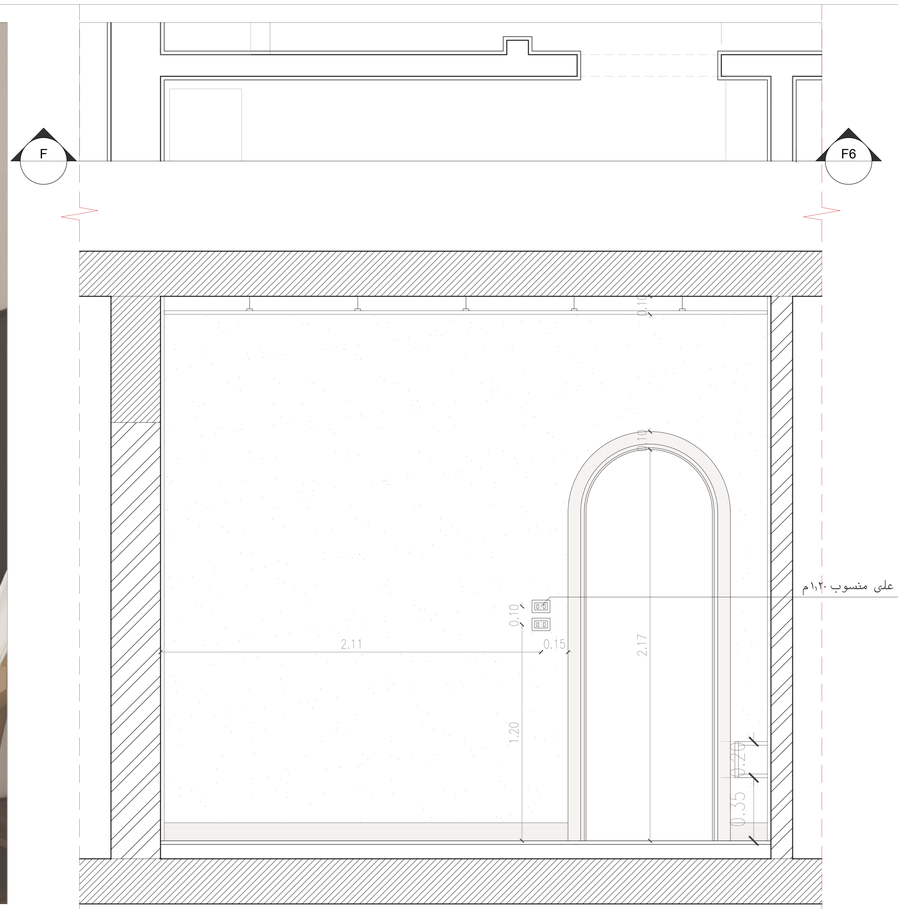

22 INTERNAL ELEVATIONS - Roof Suite

مساقط راسية - غرفة الروف

THD
STUDIO
www.THDstudio.net

CLIENT:
ا/ ايناس البيلى
MRS. Inas El Beily

TITLE:
فيـــلا سكنيـة
Residential Villa

LAVISTA DEVELOPMENTS

DRAWING :
INTERNAL ELEVATIONS
مساقط راسية

DATE:	SCALE:	PAPER:
JUN, 2026	1 : 100	A0

DRAWING BY:
ENG. BAHAELDIN AHMED

REVISED BY:
ENG. ZAHRAA SALEH

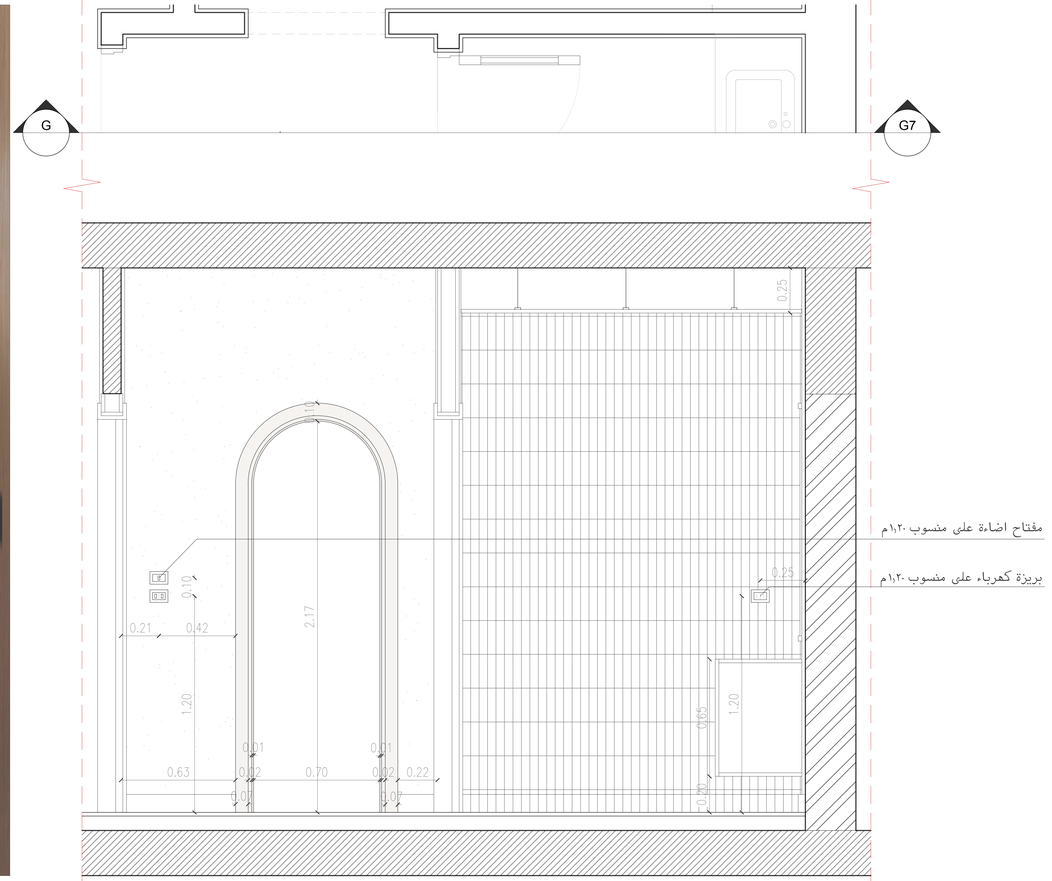

22 INTERNAL ELEVATIONS - ROOF BATHROOM

مساقط راسية - حمام الروف

THD
STUDIO
www.THDstudio.net

CLIENT:
ا / ايناس البيلى
MRS. Inas El Beily

TITLE:
فيـــلا سكنيـــة
Residential Villa

LAVISTA DEVELOPMENTS

DRAWING :
INTERNAL ELEVATIONS
مساقط راسية

DATE:	SCALE:	PAPER:
JUN, 2026	1 : 100	A0

DRAWING BY:
ENG. BAHAELDIN AHMED

REVISED BY:
ENG. ZAHRAA SALEH

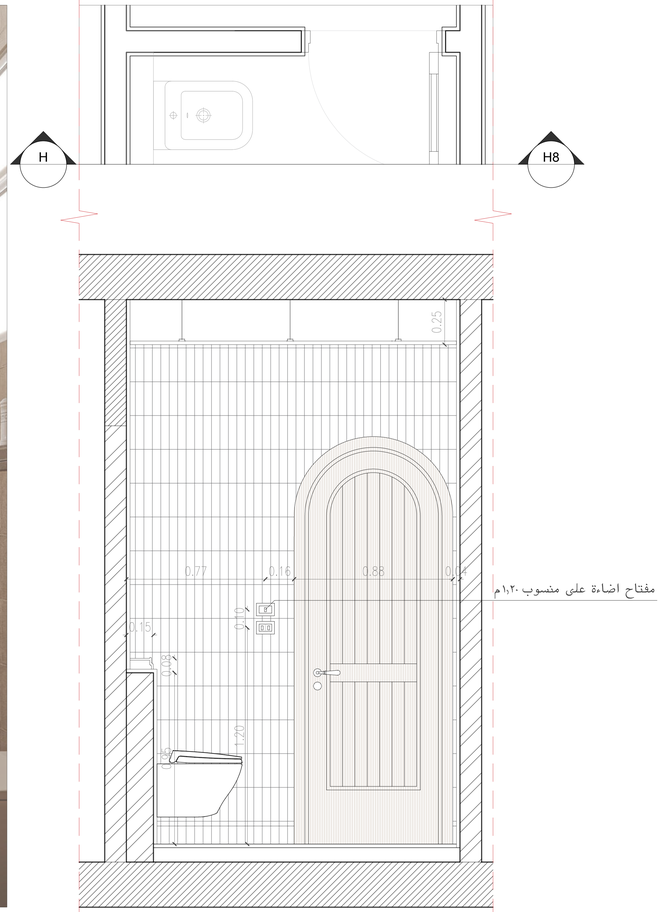

22 INTERNAL ELEVATIONS - ROOF BATHROOM

مساقط راسية - حمام الروف

THD
STUDIO
www.THDstudio.net

CLIENT:
ا/ ايناس البيلى
MRS. Inas El Beily

TITLE:
فيـــلا سكنيـــة
Residential Villa

LAVISTA DEVELOPMENTS

DRAWING :
INTERNAL ELEVATIONS
مساقط راسية

DATE:	SCALE:	PAPER:
JUN, 2026	1 : 100	A0

DRAWING BY:
ENG. BAHAELDIN AHMED

REVISED BY:
ENG. ZAHRAA SALEH