


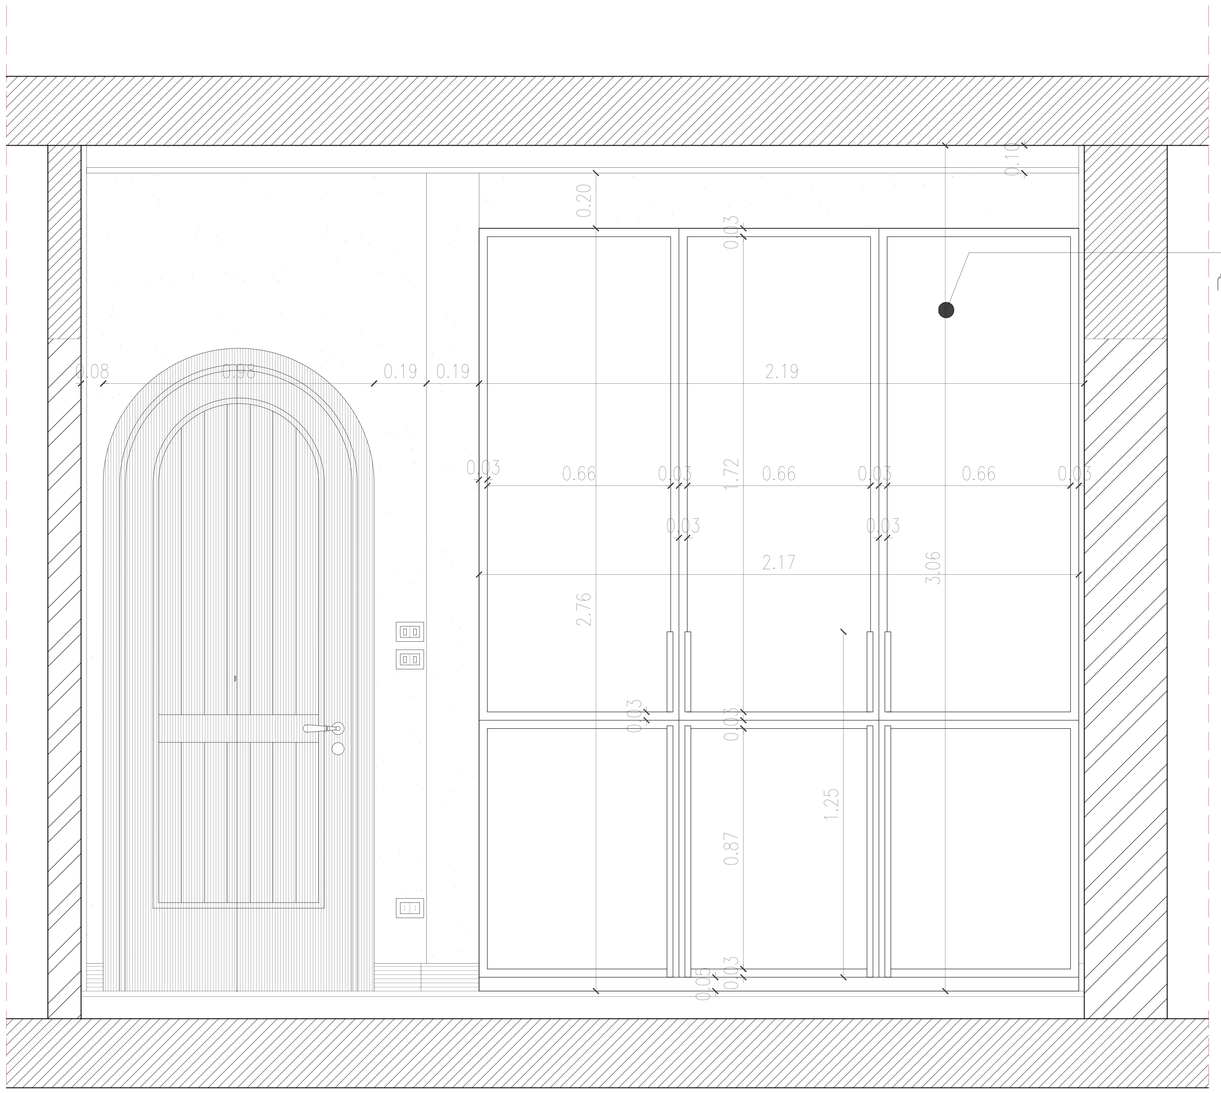

دولاب

طول ٢,٧٦ م عرض ٢,١٩ م

عمق ٠,٦٠ م

19

INTERNAL ELEVATIONS - GUEST BEDROOM

مساقط راسية - غرفة الضيوف

THD
STUDIO
www.THDstudio.net

CLIENT:
أ / ايناس البيلى
MRS. Inas El Beily

TITLE:
فيـــلا سكنيـــة
Residential Villa

LAVISTA DEVELOPMENTS


DRAWING :
INTERNAL ELEVATIONS
مساقط راسية


DATE:	SCALE:	PAPER:
JUN, 2026	1 : 100	A0

DRAWING BY:
ENG. BAHAELDIN AHMED

REVISED BY:
ENG. ZAHRAA SALEH



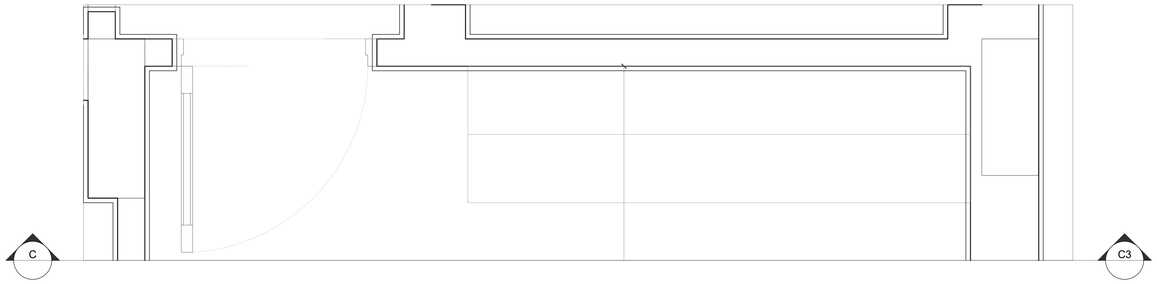

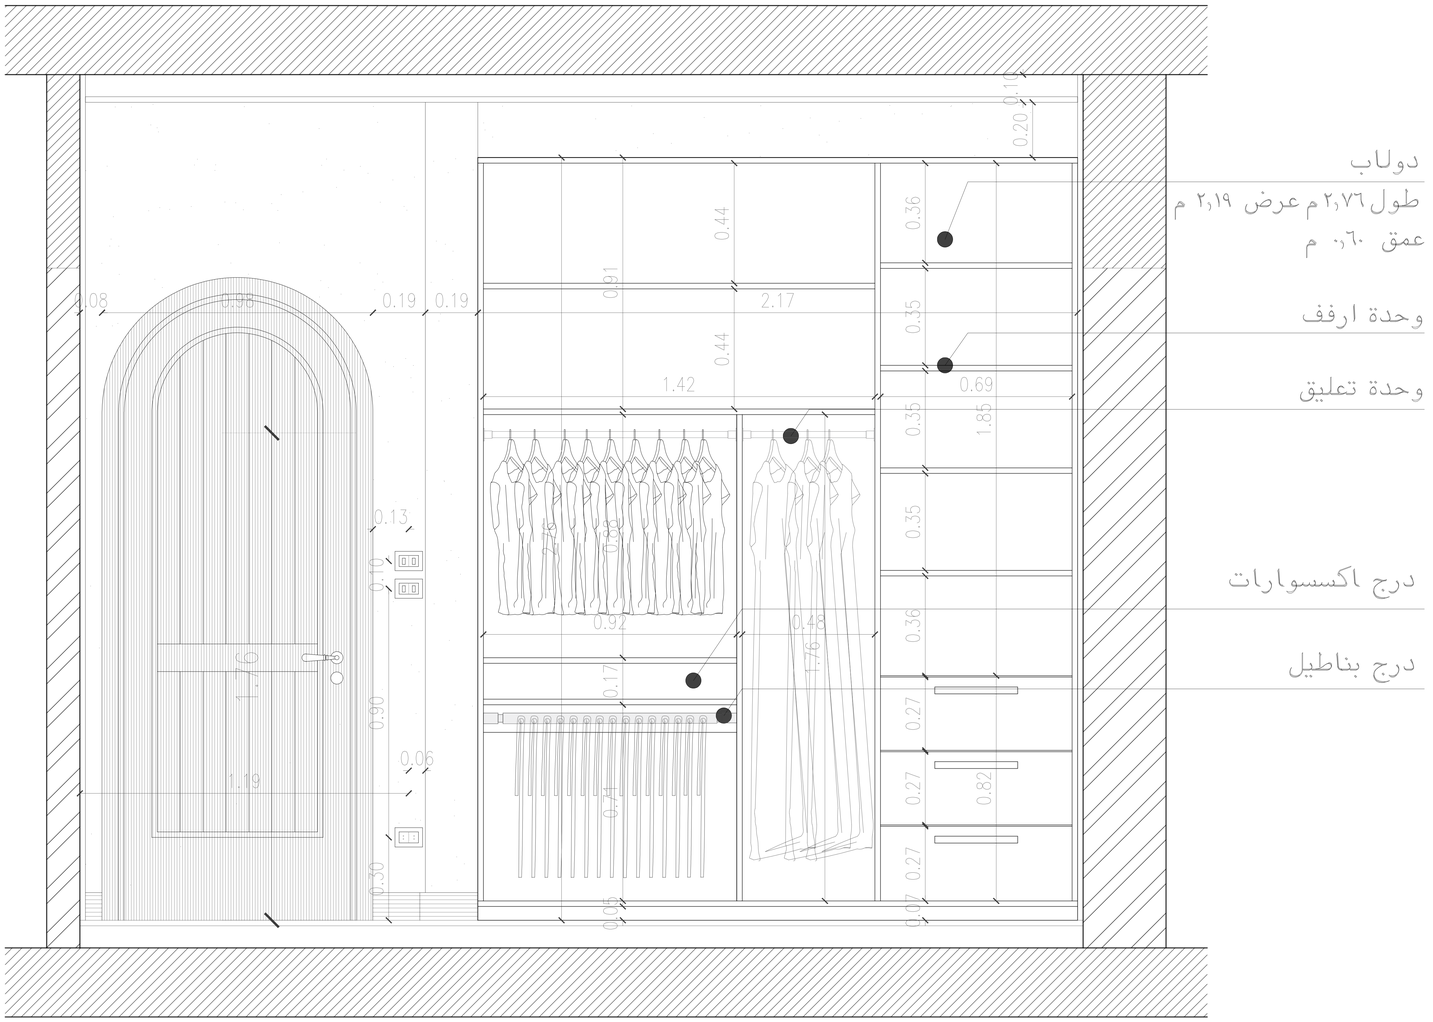

INTERNAL ELEVATIONS - GUEST BEDROOM

مساقط راسية - غرفة الضيوف

THD
STUDIO
www.THDstudio.net

CLIENT:
ا / ايناس البيلى
MRS. Inas El Beily

TITLE:
فيـــلا سكنيـــة
Residential Villa

LAVISTA DEVELOPMENTS


DRAWING :
INTERNAL ELEVATIONS
مساقط راسية

DATE:	SCALE:	PAPER:
JUN, 2026	1 : 100	A0

DRAWING BY:
ENG. BAHAELDIN AHMED

REVISED BY:
ENG. ZAHRAA SALEH



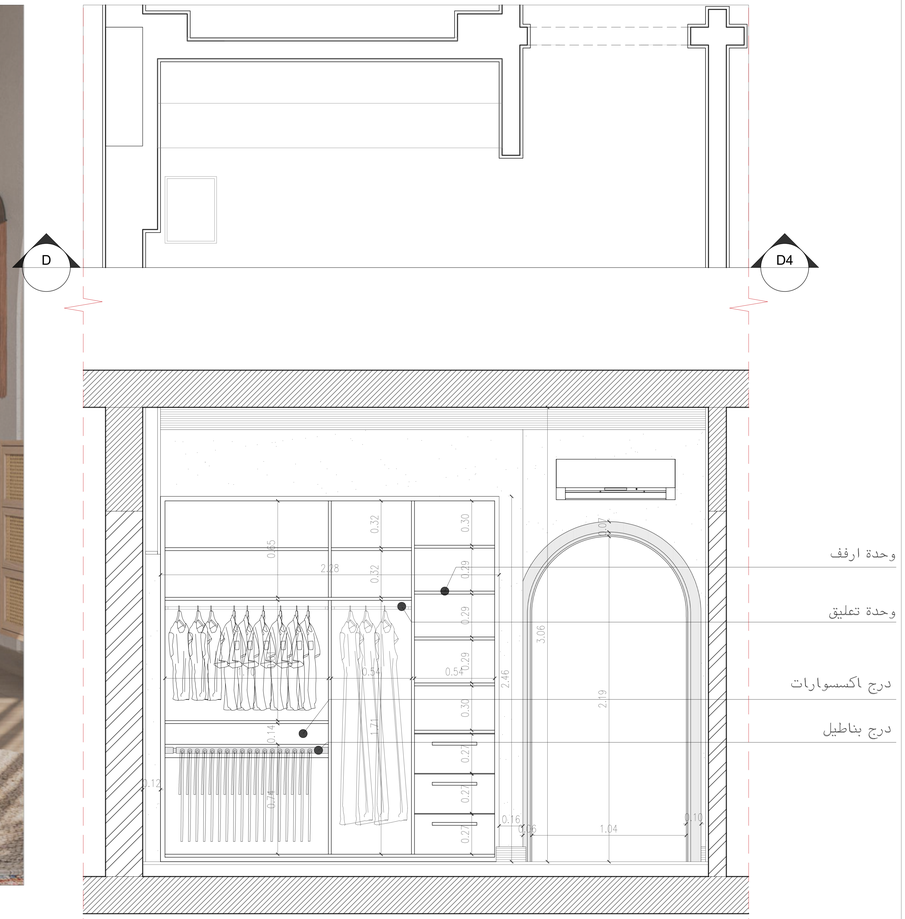

21 INTERNAL ELEVATIONS - MASTER BEDROOM

مساقط راسية - غرفة النوم الرئيسية

THD STUDIO
www.THDstudio.net

CLIENT:
ا/ ايناس البيلى
MRS. Inas El Beily

TITLE:
فيـــلا سكنيـــة
Residential Villa

LAVISTA DEVELOPMENTS


DRAWING :
INTERNAL ELEVATIONS
مساقط راسية

DATE:	SCALE:	PAPER:
JUN, 2026	1 : 100	A0

DRAWING BY:
ENG. BAHAELDIN AHMED

REVISED BY:
ENG. ZAHRAA SALEH



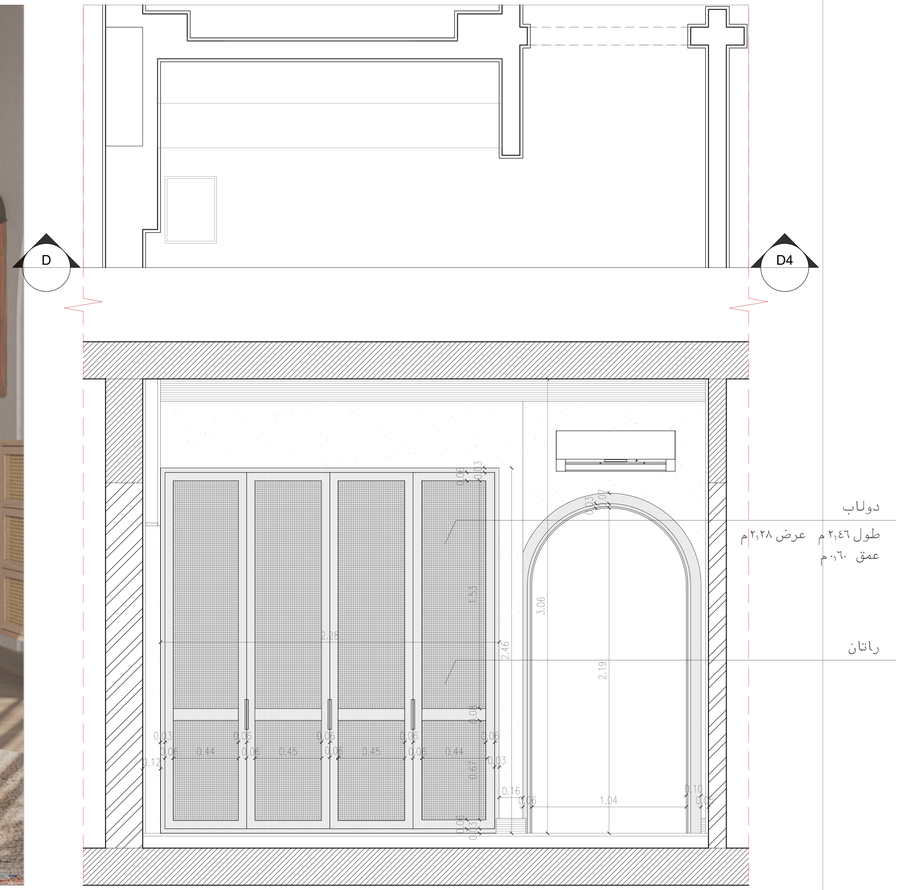

21 INTERNAL ELEVATIONS - MASTER BEDROOM

مساقط راسية - غرفة النوم الرئيسية

THD STUDIO
www.THDstudio.net

CLIENT:
ا / ايناس البيلى
MRS. Inas El Beily

TITLE:
فيـــلا سكنيـــة
Residential Villa


LAVISTA DEVELOPMENTS


DRAWING :
INTERNAL ELEVATIONS
مساقط راسية


DATE:	SCALE:	PAPER:
JUN, 2026	1 : 100	A0

DRAWING BY:
ENG. BAHAELDIN AHMED


REVISED BY:
ENG. ZAHRAA SALEH

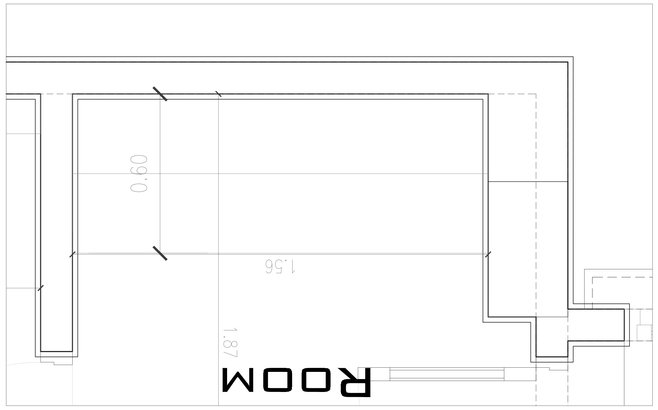

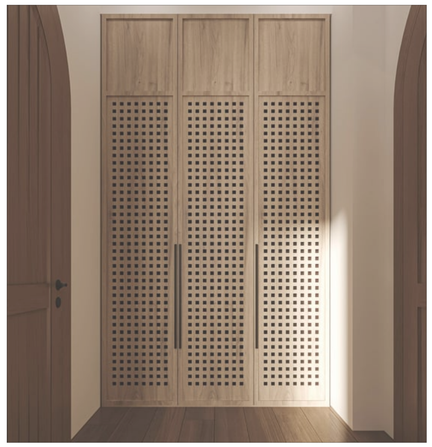

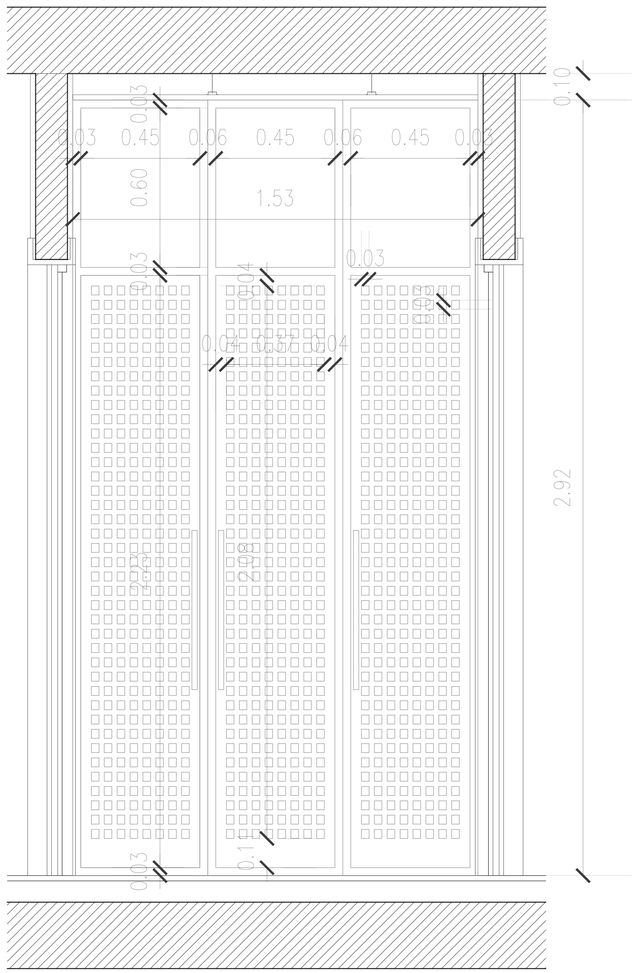
0.10
0.03
0.03
0.45
0.06
0.45
0.06
0.45
0.03
0.60
1.53
0.03
0.03
0.04
0.04
0.03
0.03
0.03



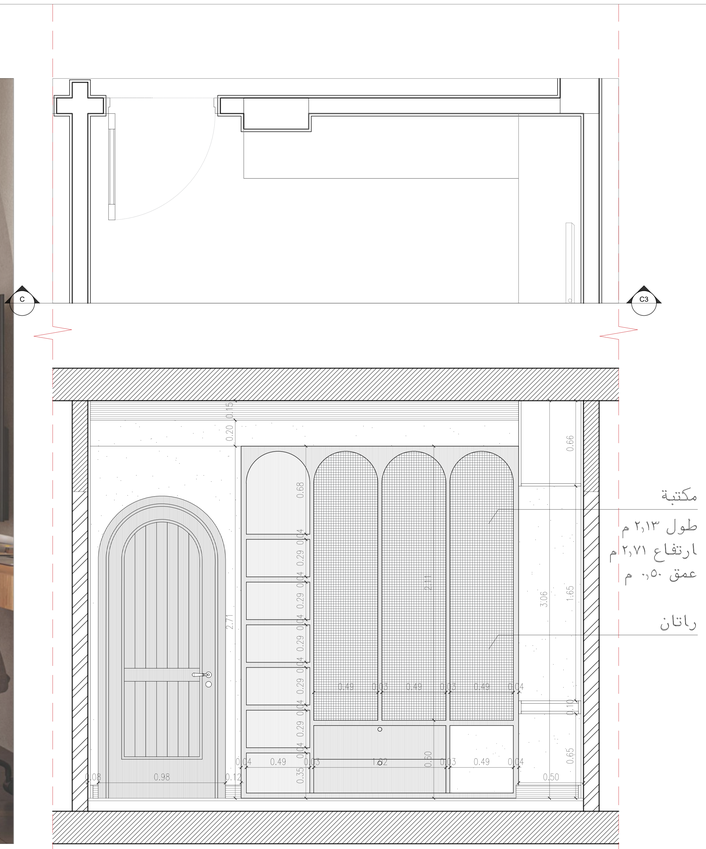

مكتبة
طول ٢٫١٣ م
ارتفاع ٢٫٧١ م
عمق ٠٫٥٠ م

راتان

INTERNAL ELEVATIONS - HOME OFFICE

مساقط راسية - المكتب

THD
STUDIO
www.THDstudio.net

CLIENT:
ا / ايناس البيلى
MRS. Inas El Beily

TITLE:
فيـــلا سكنيـــة
Residential Villa

LAVISTA DEVELOPMENTS


DRAWING :
INTERNAL ELEVATIONS
مساقط راسية

DATE:	SCALE:	PAPER:
JUN, 2026	1 : 100	A0

DRAWING BY:
ENG. BAHAELDIN AHMED

REVISED BY:
ENG. ZAHRAA SALEH



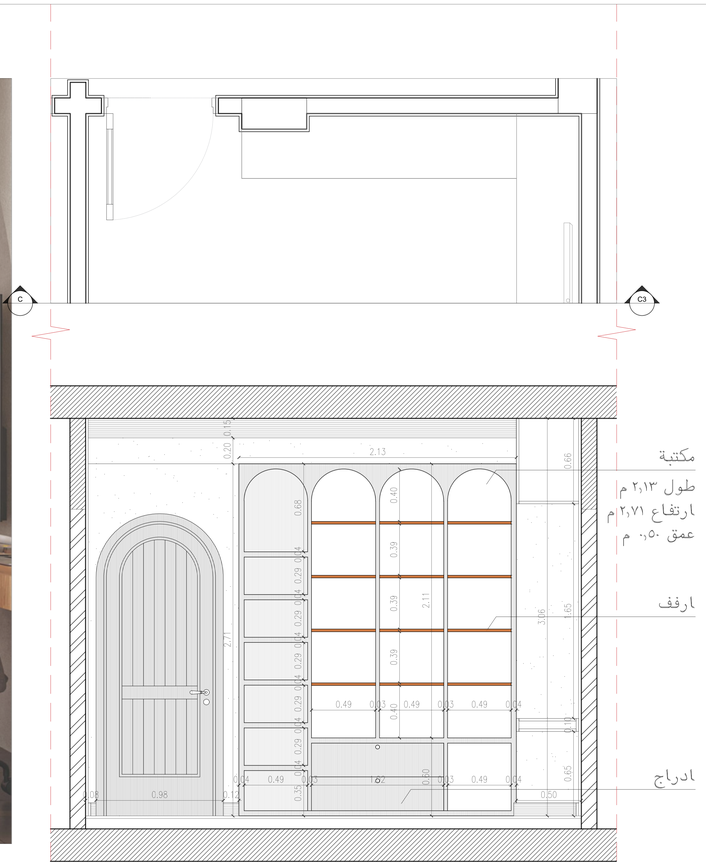

INTERNAL ELEVATIONS - HOME OFFICE

مساقط راسية - المكتب

THD
STUDIO
www.THDstudio.net

CLIENT:
ا / ايناس البيلى
MRS. Inas El Beily

TITLE:
فيـــلا سكنيـــة
Residential Villa

LAVISTA DEVELOPMENTS

DRAWING :
INTERNAL ELEVATIONS
مساقط راسية

DATE:	SCALE:	PAPER:
JUN, 2026	1 : 100	A0

DRAWING BY:
ENG. BAHAELDIN AHMED

REVISED BY:
ENG. ZAHRAA SALEH